

Общество с ограниченной ответственностью

«Арт Нуво»

107553, г. Москва, ул. Черкизовская Б., д. 30А, стр. 1. Тел. (495) 785-25-93

ОКПО96443825, ОГРН 1067746771355, ИНН/КПП 7718592726/771801001

Московский банк Сбербанка России ПАО г. Москва

Р/С № 40702810738290030078 в ПАО «Сбербанк России» г. Москва Корр. счет № 30101810400000000225

БИК 044525225

*Регистрационный номер СРО №127-091228-77 от 15.01.2010 г. Союза проектировщиков и архитекторов
в малом и среднем бизнесе (номер в государственном реестре саморегулируемых организаций
СРО-П-074-08122009)*

Новое строительство

многоэтажного гаража-стоянки

по адресу: г. Москва, Коровинское шоссе, вл. 41А, корп. 1, корп. 2

Общество с ограниченной ответственностью

«Управляющая компания «Прометей»

Рабочая документация

Раздел 5.4

«Сети связи»

Подраздел 5.4.1

«Автоматическая пожарная сигнализация.

Автоматизация»

Шифр 30.08.19-АПС

Арх. № 30.08.19-АПС

Общество с ограниченной ответственностью

«Арт Нуво»

107553, г. Москва, ул. Черкизовская Б., д. 30А, стр. 1. Тел. (495) 785-25-93

ОКПО96443825, ОГРН 1067746771355, ИНН/КПП 7718592726/771801001

Московский банк Сбербанка России ПАО г. Москва

Р/С № 40702810738290030078 в ПАО «Сбербанк России» г. Москва Корр. счет № 30101810400000000225

БИК 044525225

*Регистрационный номер СРО №127-091228-77 от 15.01.2010 г. Союза проектировщиков и архитекторов
в малом и среднем бизнесе (номер в государственном реестре саморегулируемых организаций
СРО-П-074-08122009)*

Новое строительство

многоэтажного гаража-стоянки

по адресу: г. Москва, Коровинское шоссе, вл. 41А, корп. 1, корп. 2

Общество с ограниченной ответственностью

«Управляющая компания «Прометей»

Рабочая документация

Раздел 5.4

«Сети связи»

Подраздел 5.4.1

«Автоматическая пожарная сигнализация.

Автоматизация»

Шифр 30.08.19-АПС

Арх. № 30.08.19-АПС

Генеральный директор

И.Л. Ярмак

Главный архитектор проекта

П.Н. Румянцев

Согласовано

Взам. инв. №

Подпись и дата

Инв. № подл.

Ведомость документов основного комплекта рабочих чертежей

Обозначение	Наименование	Примечание
30.08.19-АПС.ОД	Общие данные	
30.08.19-АПС.1	Схема структурная	
30.08.19-АПС.2	Автоматическая пожарная сигнализация. План расположения оборудования	3 листа
30.08.19-АПС.3	Автоматизация. План расположения оборудования	6 листов

Общие указания

1. Рабочая документация разработана в составе проектной документации «Новое строительство многоэтажного гаража-стоянки по адресу: г. Москва, Коровинское шоссе, вл.41 А, корп.1, корп.2». на основании утвержденной проектной документации по объекту, получившей положительное заключение экспертизы.

2. Нормативно-технические документы.
Применяемые нормативно-технические документы:
– Постановление Правительства РФ от 16.02.2008 № 87 «О составе разделов проектной документации и требованиях к их содержанию»;
– Федеральный закон № 123-ФЗ «Технический регламент о требованиях пожарной безопасности»;
– Федеральный закон № 384-ФЗ «Технический регламент о безопасности зданий и сооружений»;
– ГОСТ Р 21.1101-2013 «СПДС. Основные требования к проектной и рабочей документации»;
– ГОСТ 31565-2012 «Кабельные изделия. Требования пожарной безопасности»;
– ПУЭ «Правила устройства электроустановок. Издание 7»;
– СП 5.13130.2009 «Установки пожарной сигнализации и пожаротушения автоматические. Нормы и правила проектирования»;
– СП 6.13130.2013 «Системы противопожарной защиты. Электрооборудование. Требования пожарной безопасности»;
– СП 134.13330.2012 «Системы электросвязи зданий и сооружений. Основные положения проектирования»;
– Руководящий документ 78.145-93 Руководящий документ «Системы и комплексы охранной, пожарной и охранно-пожарной сигнализации. Правила производства и приемки работ»;
– Пособие к РД 78.145-93 «Системы и комплексы охранной, пожарной и охранно-пожарной сигнализации. Правила производства и приемки работ».

3. Назначение системы автоматической пожарной сигнализации и автоматизации.
Система автоматической пожарной сигнализации (АПС) предназначена обнаружения пожара на ранней стадии в помещениях объекта, система автоматизации предназначена для обнаружения загазованности в помещении автостоянки и управления оборудованием противопожарной защиты при пожаре, управлением вентиляцией и СОУЭ. Предусмотрено управление АПС и системой автоматизации с сервера АПС с использованием специализированного программного обеспечения.

4. Состав, алгоритм работы и размещение оборудования АПС и автоматизации
Состав АПС:
– пульт контроля и управления «С2000М»;
– контроллеры двух проводной линии «С2000-КДЛ»;
– извещатели пожарные дымовые адресно-аналоговые ИП 34А;
– извещатели пожарные ручные адресные ИПР 513-ЗАМ;
– устройство оконечное объектное системы передачи извещений С2000-PGE;
– резервированные источники питания (РИП);
– сервер пожарной сигнализации и системы контроля доступа ОПС-СКД127 исп.02.
Состав системы автоматизации:
– контроллеры двух проводной линии «С2000-КДЛ»;

Технические решения, принятые в рабочих чертежах, соответствуют требованиям экологических, санитарно-гигиенических, противопожарных и других норм, действующих на территории Российской Федерации, и обеспечивают безопасную для жизни и здоровья людей эксплуатацию объекта при соблюдении предусмотренных рабочими чертежами мероприятий.

Главный инженер проекта  И.Л. Ярмак

Обозначение	Наименование	Примечание
	<u>Ссылочные документы</u>	
	<u>Прилагаемые документы</u>	
30.08.19-АПС.СО	Спецификация оборудования, изделий и материалов	3 листа

– извещатели газовые адресно-аналоговые С2000-ИПГ;
– адресные расширители С2000-АР2;
– адресные расширители С2000-АР8;
– длоки сигнально-пусковые С2000-СП1 исп. 01;
– длоки сигнально-пусковые адресные С2000-СП4;
– длоки сигнально-пусковые адресные С2000-СП2;
– извещатели газовые адресно-аналоговые С2000-ИПГ;
– резервированные источники питания (РИП).

При поступлении сигнала от пожарных дымовых адресно-аналоговых извещателей ИП 34А или пожарных ручных адресных извещателей ИПР 513-ЗАМ, включенных в двухпроводные кольцевые адресные шлейфы С2000-КДЛ, пульт контроля и управления С2000М формирует сигнал “ПОЖАР”. По интерфейсу RS-485 сигнал пожар поступает в систему автоматизации, в систему оповещения и управления эвакуацией людей при пожаре и на устройство оконечное объектное системы передачи извещений С2000-PGE для передачи сигнала о пожаре на пульт «112» ЦУКС МЧС России по г. Москве.

Приборы системы автоматизации подключены к пульту контроля и управления С2000М АПС по интерфейсу RS-485 напрямую или через контроллеры двухпроводной линии С2000-КДЛ.

При поступлении сигнала «ПОЖАР» от пульта контроля и управления С2000М АПС система автоматизации по запрограммированной логике формирует адресные управляющие сигналы в для:

– отключения общеобменной вентиляции;
– включения противодымной вентиляции;
– управления клапанами общеобменной и противодымной вентиляций;
– открытие соленоидных клапанов дренажных завес;
– закрытия ворот, разделяющих пожарные отсеки.

Блоки сигнально-пусковые С2000-СП4 предназначены для управления клапанами клапанами общеобменной и противодымной вентиляции, клапанами дренажных завес, выдачи управляющих сигналов на щиты электроснабжения.

Блоки сигнально-пусковые С2000-СП2 предназначены для управления приводами ворот, разделяющими пожарные отсеки.

Блоки сигнально-пусковые С2000-СП1 предназначены для выдачи управляющих сигналов на шкафы управления для отключения тепловых завес и общеобменной вентиляции.

Адресные расширители С2000-АР2 предназначены для получения сигналов “Авария” и “Работа” со шкафов управления.

Адресные расширители С2000-АР8 предназначены для получения сигналов “Открыто” и “Закрыто” с магнитоcontactных извещателей, установленных на воротах, разделяющих пожарные отсеки.

При поступлении сигнала загазованности (срабатывание извещателей газовых адресно-аналоговых С2000-ИПГ), система автоматизации формирует адресные управляющие сигналы в систему автоматики (по запрограммированной логике), для:

– включения общеобменной вентиляции (при отсутствии пожара на объекте);
– включение СОУЭ.

Планы размещения оборудования АПС смотреть на чертежах 30.08.19-АПС.2

Пульт контроля и управления «С2000М», контроллеры двух проводной линии «С2000-КДЛ» и длоки питания установить в помещении охраны на стене на высоте 1,5м до органов управления и индикации.

Извещатели пожарные дымовые адресно-аналоговые ИП 34А установить на перекрытиях здания, извещатели пожарные ручные адресные ИПР 513-ЗАМ установить на колоннах и стенах здания. Расстановку извещателей произвести согласно планов расстановки оборудования в соответствии с требованиями СП 5.13130.2009.

Планы размещения оборудования системы автоматизации смотреть на чертежах 30.08.19-АПС.3.

Контроллеры двух проводной линии «С2000-КДЛ» и длоки питания установить в помещении охраны на стене на высоте 1,5 м от уровня чистого пола до органов управления и индикации.

Все длоки сигнально-пусковые должны быть установлены в непосредственной близости от объектов

управления. Адресные расширители установить в непосредственной близости от мест получения сигналов. Блоки питания, предназначенные для электроснабжения сигнально-пусковых блоков, расположить в непосредственной близости от объектов электроснабжения. В помещении автостоянки и на путях эвакуации оборудование установить на высоте не менее 2 м от уровня чистого пола до нижней кромки оборудования, в остальных помещениях оборудование установить на стене на высоте 1,5 м от уровня чистого пола до органов управления и индикации.

Газовые адресно-аналоговые извещатели С2000-ИПГ устанавливаются на колоннах в помещении автостоянки на высоте 1,3-1,5 м от уровня чистого пола согласно планов расстановки оборудования.

Магнито-контактные извещатели установить на воротах, разделяющих пожарные отсеки, для отслеживания положения ворот в крайних положениях.

5. Электропитание и заземление АПС

Согласно СП 6.13130.2013 электропитание АПС осуществляется от отдельной группы напряжением ~ 220 В по первой категории электроснабжения согласно ПУЭ Издание 7. Подключение оборудования АПС к электрической сети ~220 В смотреть в томе марки ЗОМ.

Для защиты обслуживающего персонала от поражения электрическим током металлические корпуса оборудования и водо-газопроводные трубы должны быть заземлены.

Заземление оборудования выполнить металлическим соединением их корпусов с защитным проводником сети электроснабжения, для чего использовать защитные жилы питающих кабелей, защитные провода и специально проложенные для этой цели проводники. Сопротивление заземляющего устройства, используемого для заземления электрооборудования, должно быть не более 4 Ом. В цепи заземляющих проводников не должно быть разъедающих приспособлений и предохранителей.

Присоединение заземляющих проводников к частям электрооборудования должно быть выполнено сваркой или болтовым соединением, в соответствии с ПУЭ Издание 7.

6. Кабельные линии

Типы кабелей и способы их прокладки выбраны в соответствии с требованиями Технического регламента о требованиях пожарной безопасности, ГОСТ 31565-2012 и технической документацией на приборы и оборудование системы.

Кабельные линии прокладываются по стенам и перекрытиям, место прокладки кабелей уточнить по месту при монтаже.

Для защиты от механических повреждений кабельные линии проложить внутри пожарного отсека в жестких ПВХ-трубах, транзитные кабели, идущие в другой пожарный отсек, проложить в водо-газопроводной трубе, кабели в помещении слабых токов и в помещении диспетчерской в электротехническом коробе. Для крепления ПВХ-труб и водо-газопроводных труб применить двухлапковые скобы. В местах поворота водо-газопроводной трубы установить протяжные кородки. Подключение магнитоcontactных извещателей произвести через монтажные огнестойкие коробки КМ-О (4к)-IP41, установленные в распаячные коробки.

Перед производством работ произвести промер трасс прокладки кабелей.



Кабели прокладываются отдельно от остальных кабелей и проводов. Не допускается совместная прокладка шлейфов и соединительных линий с линиями напряжением 110 В и более в одном коробе, трубе, жгуте, замкнутом канале строительной конструкции или на одном лотке.

7. Мероприятия по охране труда и безопасной эксплуатации



При монтаже оборудования необходимо соблюдать инструкции заводов-изготовителей изделий, а также ПУЭ. Издание 7 и “Правила эксплуатации электроустановок потребителей”.

Для защиты обслуживающего персонала от поражения электрическим током при повреждении изоляции необходимо предусмотреть заземление металлических корпусов оборудования и трубопроводов.

Для заземления оборудования использовать защитные жилы питающих кабелей, защитные провода и специально проложенные для этой цели проводники. Присоединение заземляющих проводников к частям электрооборудования должно быть выполнено сваркой или болтовым соединением, в соответствии с ПУЭ. Издание 7.

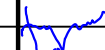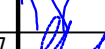							Шифр:	30.08.19-АПС.ОД				
							Заказчик:	ООО “Управляющая компания Прометей”				
							Новое строительство многоэтажного гаража-стоянки по адресу: г. Москва, Коровинское шоссе, вл.41 А, корп. 1, корп. 2					
Изм.	Кол. уч.	Лист	№ док.	Подп.	Дата	Автоматическая пожарная сигнализация. Автоматизация		Стадия	Лист	Листов		
Разраб.		Новиков			17.02.20			Р		1		
Пров.		Ярмак И Л			17.02.20							
						Общие данные		ООО “Арт Нуво”				
Н.контр.		Румянцев			17.02.20							
ГИП		Ярмак И Л			17.02.20							

Формат А3

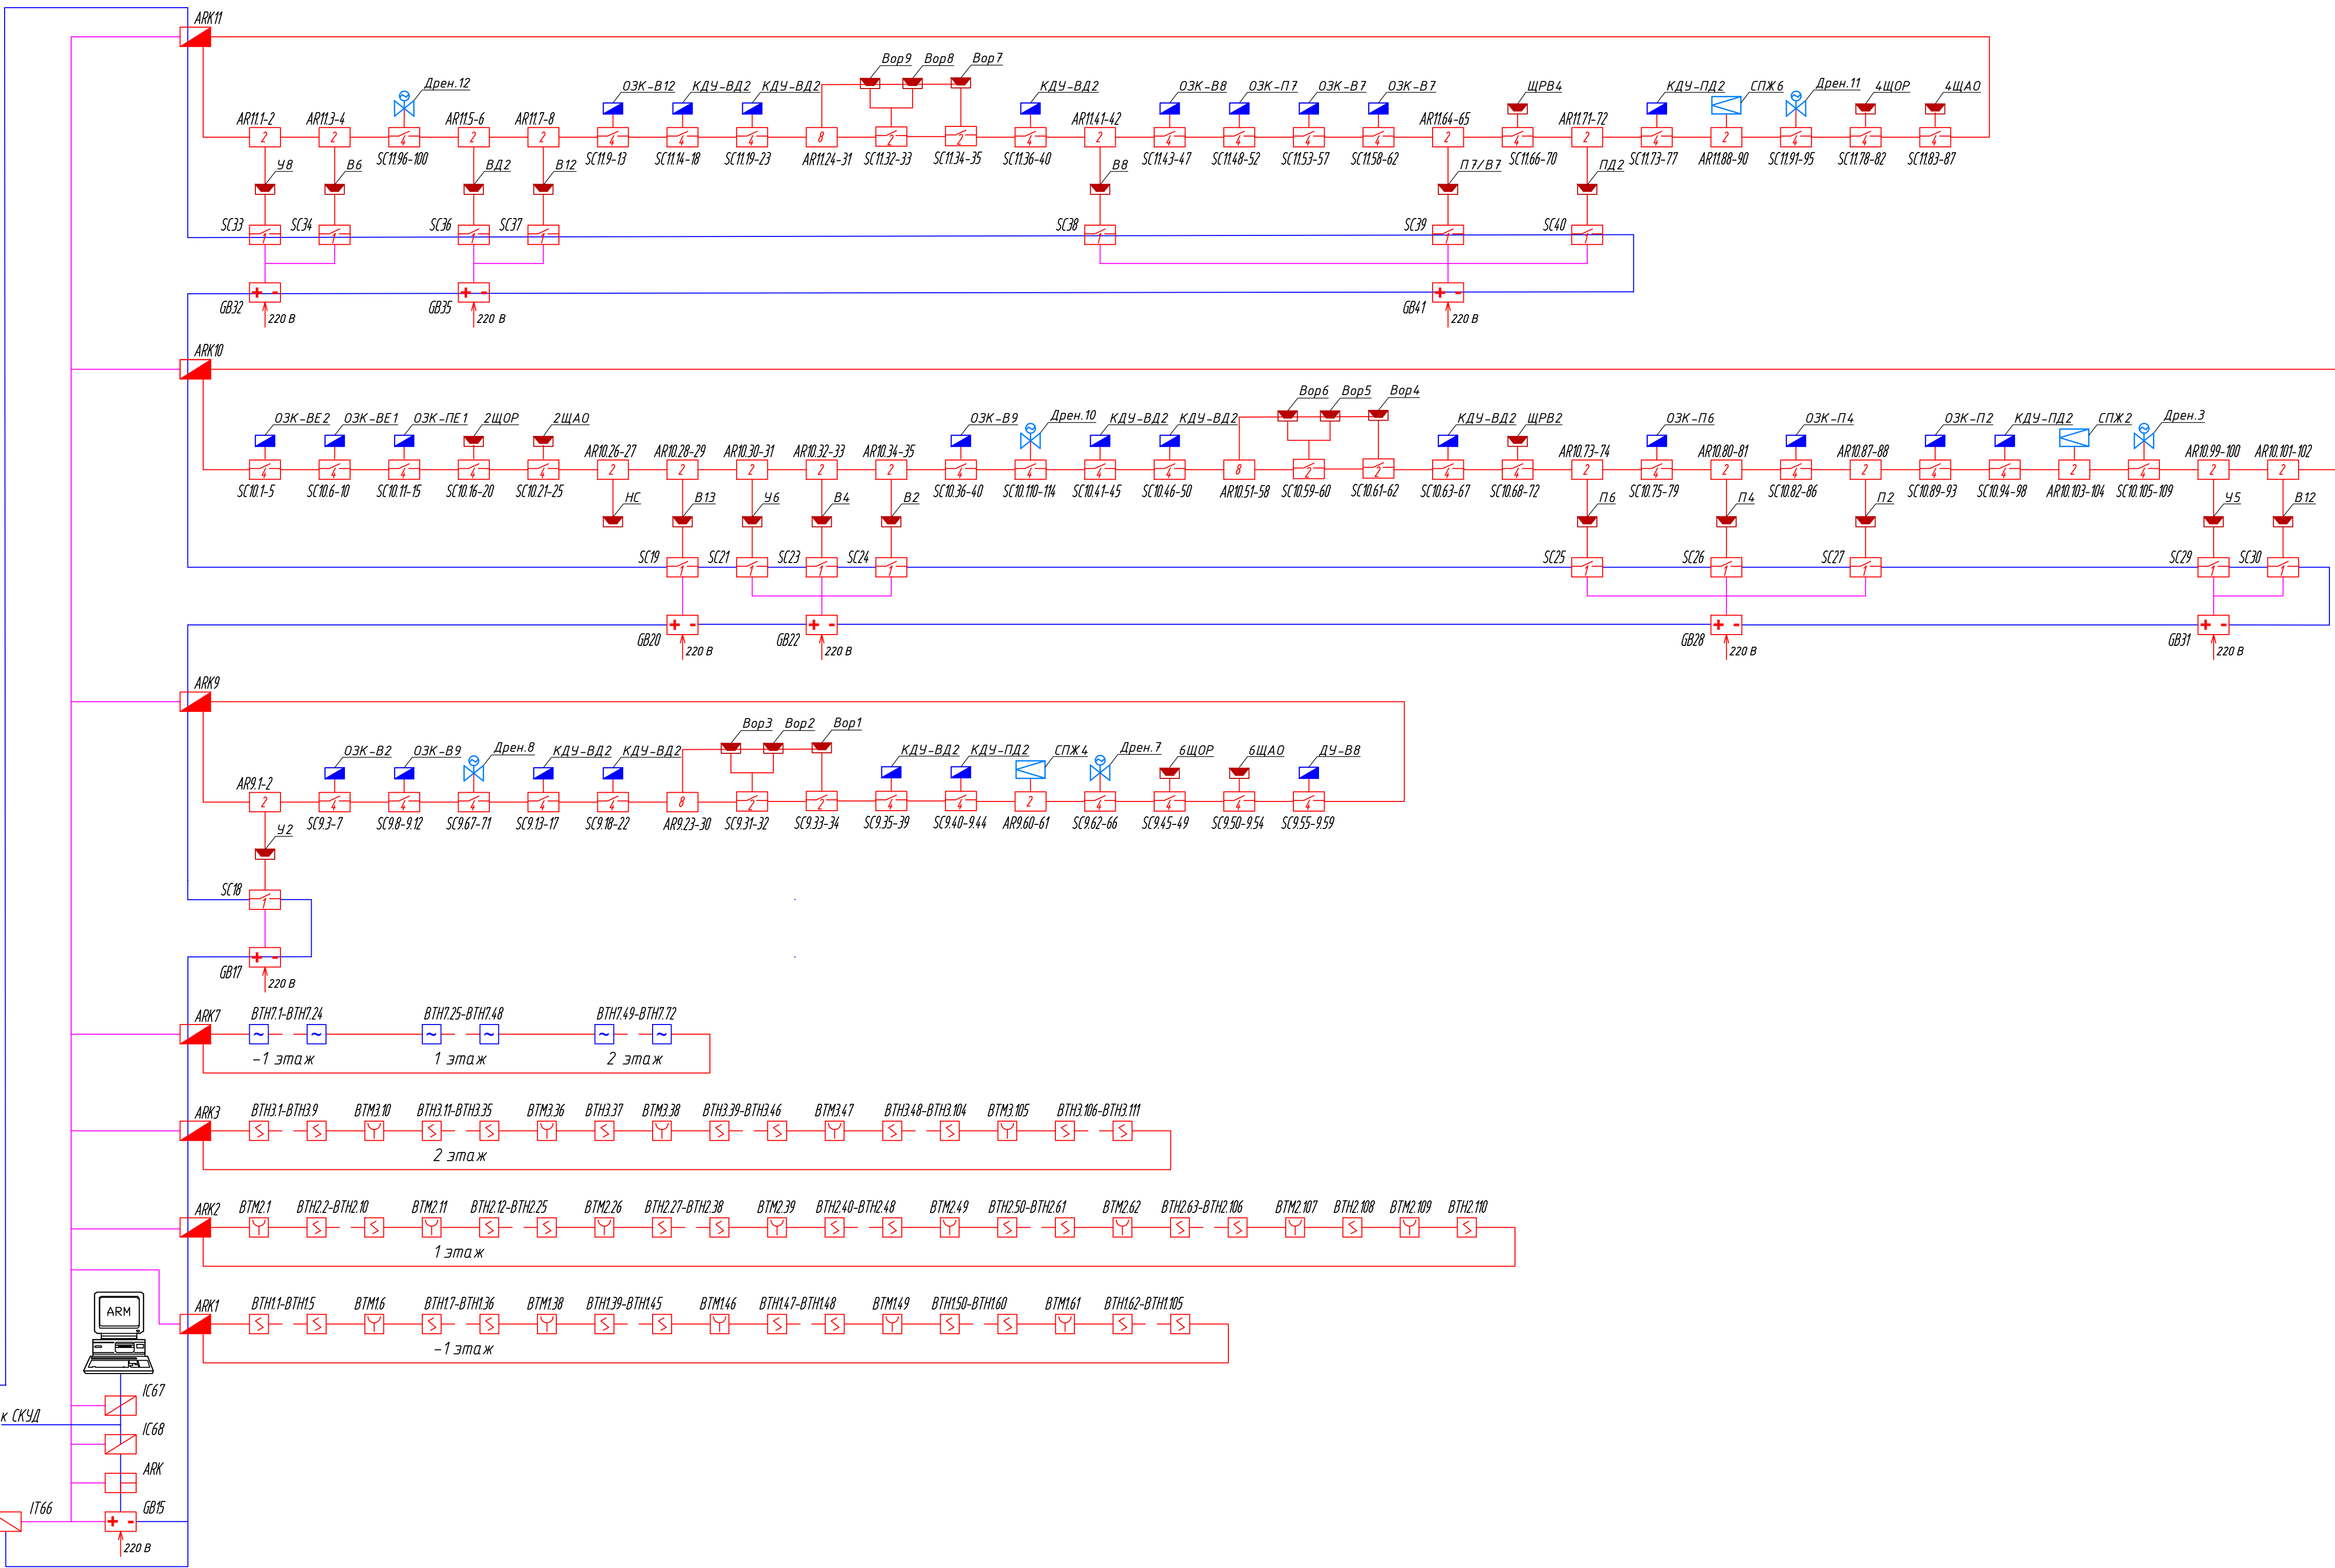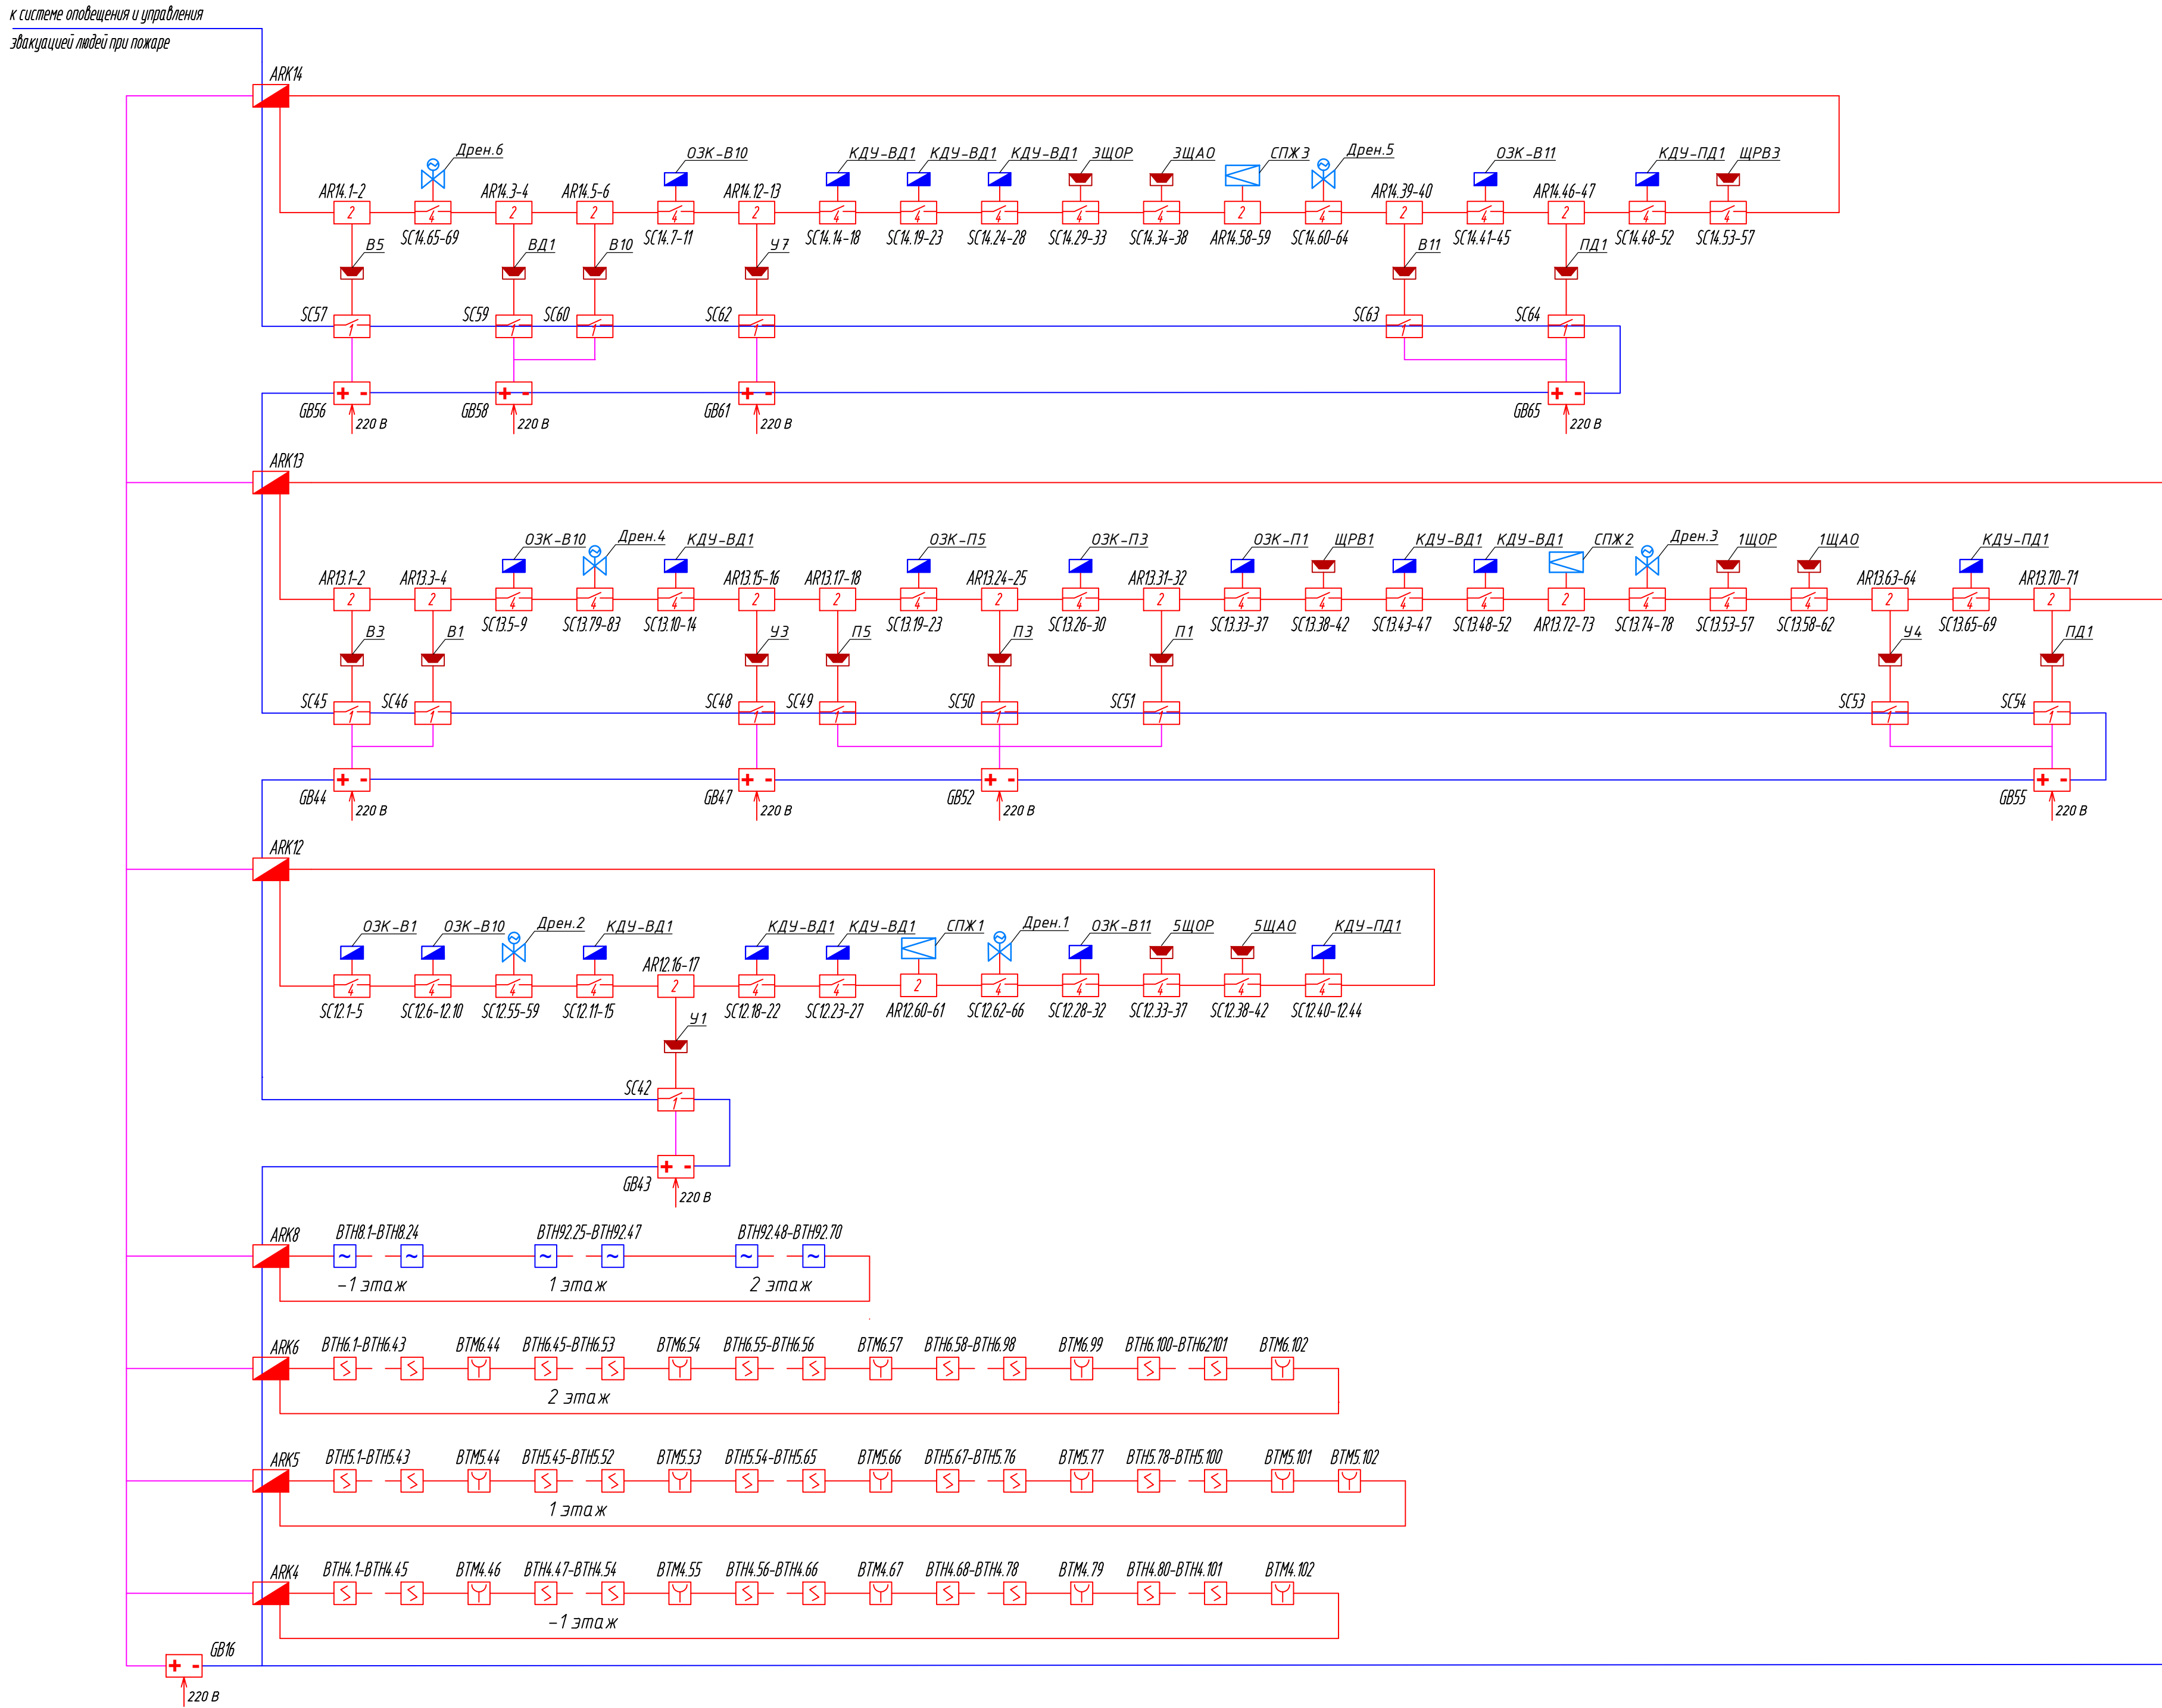

Условные обозначения

- Пульт контроля и управления С2000М
- Информатор телефонный для сетей сотовой связи С2000-РGE
- Преобразователь интерфейса С2000-ПИ
- Контроллер двухпроводной линии С2000-КДЛ
- Контрольно-пусковой блок С2000-КПБ системы оповещения
- Блок сигнально-пусковой С2000-СП1
- Блок сигнально-пусковой адресный С2000-СП4
- Блок питания РИП-24 исп. 50

Извещатель пожарный дымовый адресный ДИП-34АИзвещатель пожарный ручной адресный ИПР 513-3АМИзвещатель газовый адресный С2000-ИГПШкаф электропитания, управления вентиляцией или инженерным оборудованиемКлапан огнезадерживающий или дымоудаленияКран с электроприводомСигнализатор потока жидкостиШлейфы пожарной сигнализации и управленияИнтерфейс RS-485Кабель электропитания 24 ВАвтоматизированное рабочее место

Общие данные см. 30.08.19-АПС.0Д

Шифр: 30.08.19-АПС.1					
Заказчик: ООО "Управляющая компания Прометей"					
Новое строительство многоэтажного гаража-стоянки по адресу: г. Москва, Карамзинское шоссе, вл.41 А, корп.1, корп.2					
Изм.	Кол. вч.	Лист	М. вх.	Подп.	Дата
Разраб.	Новиков	1	17.02.20	17.02.20	17.02.20
Проб.	Ярнав И. И.	1	17.02.20	17.02.20	17.02.20
Автоматическая пожарная сигнализация. Автоматизация				Стадия	Лист
Схема структурная				Р	1
Н. контр. Рязанцев				ООО "Арт Нуво"	
ГИП Ярнав И. И.				Формат: А2х3 Альбомный	

План -1 этажа

Экспликация помещений

№	Наименование помещений	Площадь м²	Категория взрывопожарной и пожарной опасности
001	Автостоянка №1	2057,6	B1
002	Автостоянка №2	2133,3	B1
003	Помещение хранения пож. инвентаря	16,0	B4
004	Пом. хранения уборочного инвентаря	12,7	B4
005	Пом. хранения уборочного инвентаря	12,7	B4
006	Помещение хранения пож. инвентаря	15,9	B4




Общие данные см. 30.08.19-АПС.02
Условные обозначения см. 30.08.19-АПС.1

						Шифр: 30.08.19-АПС.2		
						Заказчик: ООО "Управляющая компания Прометей"		
						Новое строительство многоэтажного гаража-стоянки по адресу: г. Москва, Коробинское шоссе, вл.41 А, корп.1, корп.2		
Изм.	Кол.уч.	Лист	№ док.	Подп.	Дата	Автоматическая пожарная сигнализация	Стадия	Лист
Разраб.		Новиков	4.02.20				Р	1
Проб.		Ярмак И.Л.	17.02.20					3
						План расположения оборудования	ООО "Арт Нуво"	
Н.контр.		Румянцев	17.02.20					
ГИП		Ярмак И.Л.	17.02.20					

Составлено					
Взам. инв. №					
Подпись и дата					
Инв. № подл.					

Экспликация помещений			
№	Наименование помещений	Площадь м²	Категория взрывопожарной и пожарной опасности
101	Автостоянка №3	1982,2	В1
102	Автостоянка №4	2088,9	В1
103	Помещение охраны, диспетчерская	29,6	
104	Помещение слабых токов	10,9	В3
105	Электрощитовая	20,8	В3
106	Насосная	62,6	В4
107	Помещение хранения пож. инвентаря	12,7	В4
108	Пом. хранения уборочного инвентаря	12,7	В4
109	Помещение вент. установки	62,6	В1
110	Коридор	12,6	
111	С.у.	4,5	
112	С.у.	4,5	
113	Комната хранения багажа	25,9	В3
114	Помещение вент. установки	62,4	В1
115	Коридор	12,6	
116	С.у. для инвалидов	4,5	
117	С.у.	4,5	

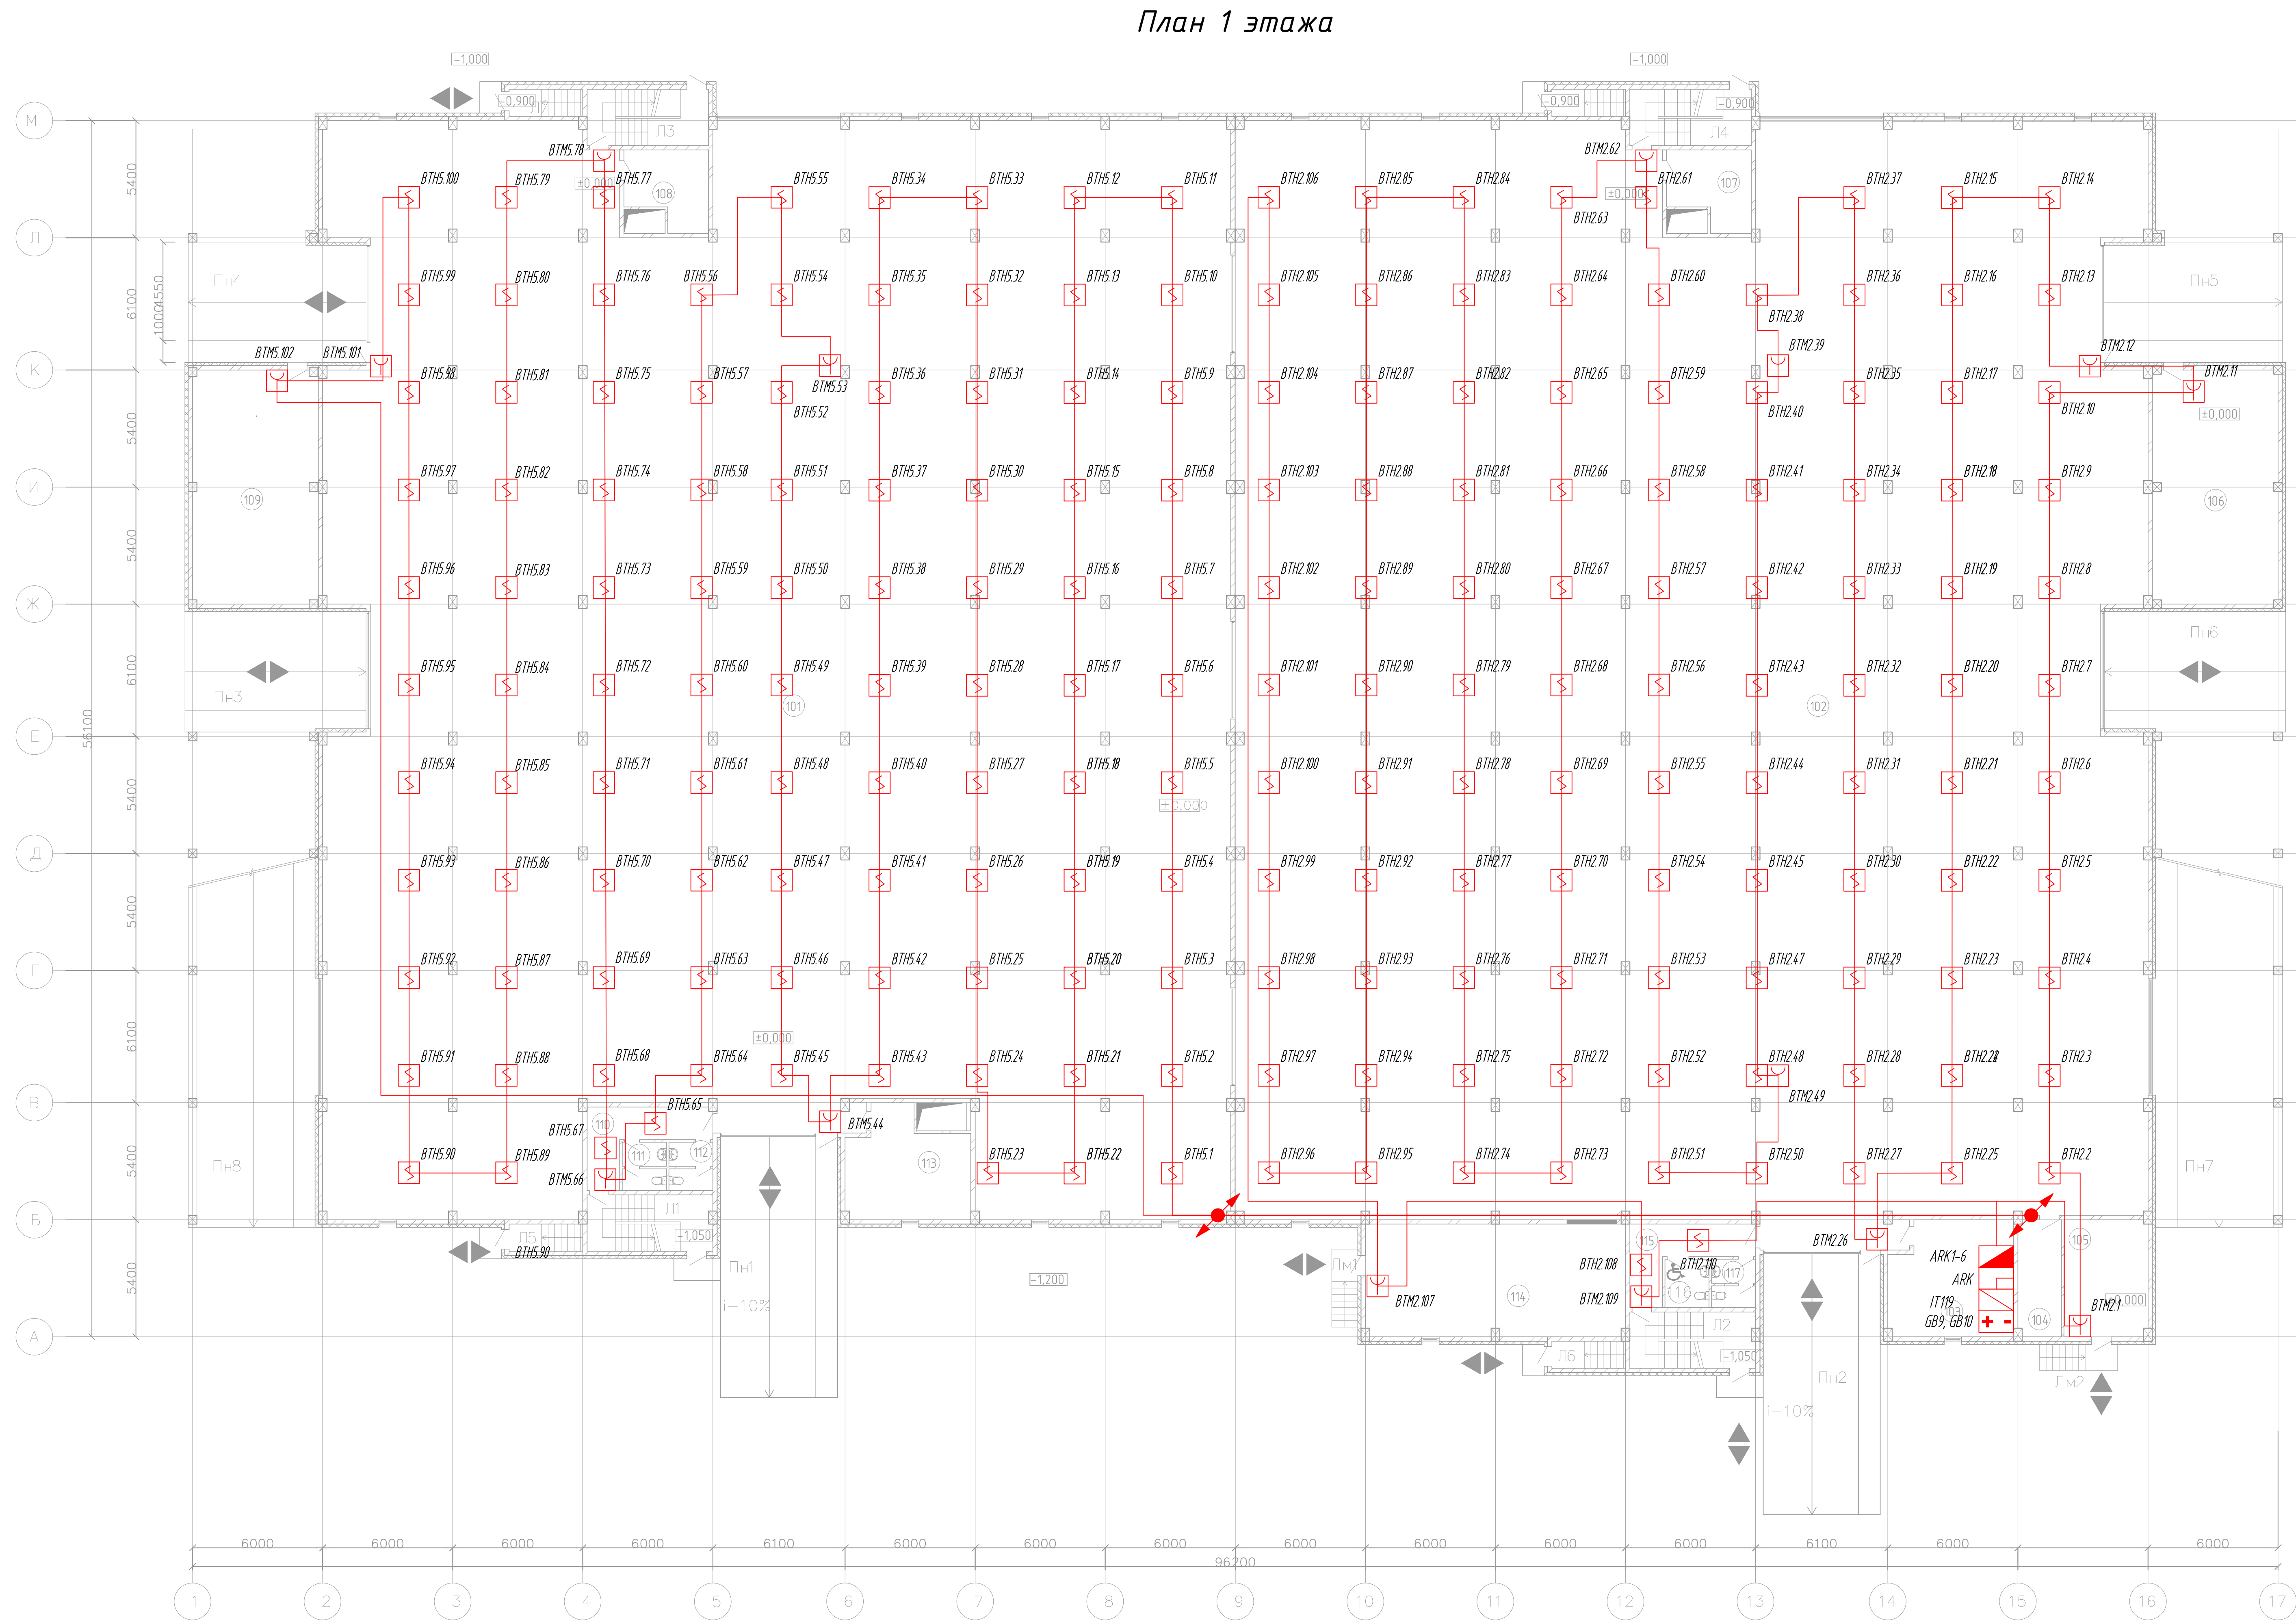

Шифр:						30.08.19-АПС.2		
Заказчик: ООО "Управляющая компания Прометей"								
Новое строительство многоэтажного гаража-стоянки по адресу: г. Москва, Коробинское шоссе, вл.41 А, корп.1, корп.2								
Изм.	Кол. изм.	Лист	№ док.	Подп.	Дата	Автоматическая пожарная сигнализация	Стадия	Лист
Разраб.		Новиков	4.02.20	И.Л.	17.02.20		Р	2
Проб.		Ярмак	И.Л.	И.Л.	17.02.20	План расположения оборудования	Лист	Листов
							3	3
Н.контр.		Румянцев	17.02.20	И.Л.	17.02.20	План расположения оборудования	ООО "Арт Нуво"	
ГИП		Ярмак	И.Л.	И.Л.	17.02.20			

578-558-608-586-578-580-3478-158-4000

План 2 этажа

Экспликация помещений

№	Наименование помещений	Площадь м²	Категория взрывопожарной и пожарной опасности
201	Автостоянка №5	2000,4	В1
202	Автостоянка №6	2120,3	В1
203	Пом. хранения уборочного инвентаря	31,2	В4
204	Вентиляционная камера	26,3	В1
205	Коридор	11,4	
206	С.у.	5,0	
207	С.у.	5,0	
208	Бухгалтерия	20,1	
209	Секретариат	28,5	
210	Дирекция	31,2	
211	Пом. хранения уборочного инвентаря	12,4	В4
212	Пом. хранения уборочного инвентаря	12,4	В4
213	Коридор	12,6	
214	С.у.	5,0	
215	С.у.	5,0	
216	Пом. хранения уборочного инвентаря	30,8	В4
217	Вентиляционная камера	27,5	В1




Составлено					
Взам. инв. №					
Подпись и дата					
Инв. № подл.					

						Шифр: 30.08.19-АПС.2		
						Заказчик: ООО "Управляющая компания Прометей"		
						Новое строительство многоэтажного гаража-стоянки по адресу: г. Москва, Коробинское шоссе, вл.41 А, корп.1, корп.2		
Изм.	Кол.уч.	Лист	№ док.	Подп.	Дата	Автоматическая пожарная сигнализация	Стадия	Лист
Разраб.							Р	3
Проб.						План расположения оборудования	Листов	
							3	
Н.контр.	Румянцев	7.02.20				План расположения оборудования	ООО "Арт Нуво"	
ГИП	Ярмак И.П.	7.02.20						

План -1 этажа

Экспликация помещений

№	Наименование помещений	Площадь м²	Категория взрывопожарной и пожарной опасности
001	Автостоянка №1	2057,6	B1
002	Автостоянка №2	2133,3	B1
003	Помещение хранения пож. инвентаря	16,0	B4
004	Пом. хранения уборочного инвентаря	12,7	B4
005	Пом. хранения уборочного инвентаря	12,7	B4
006	Помещение хранения пож. инвентаря	15,9	B4

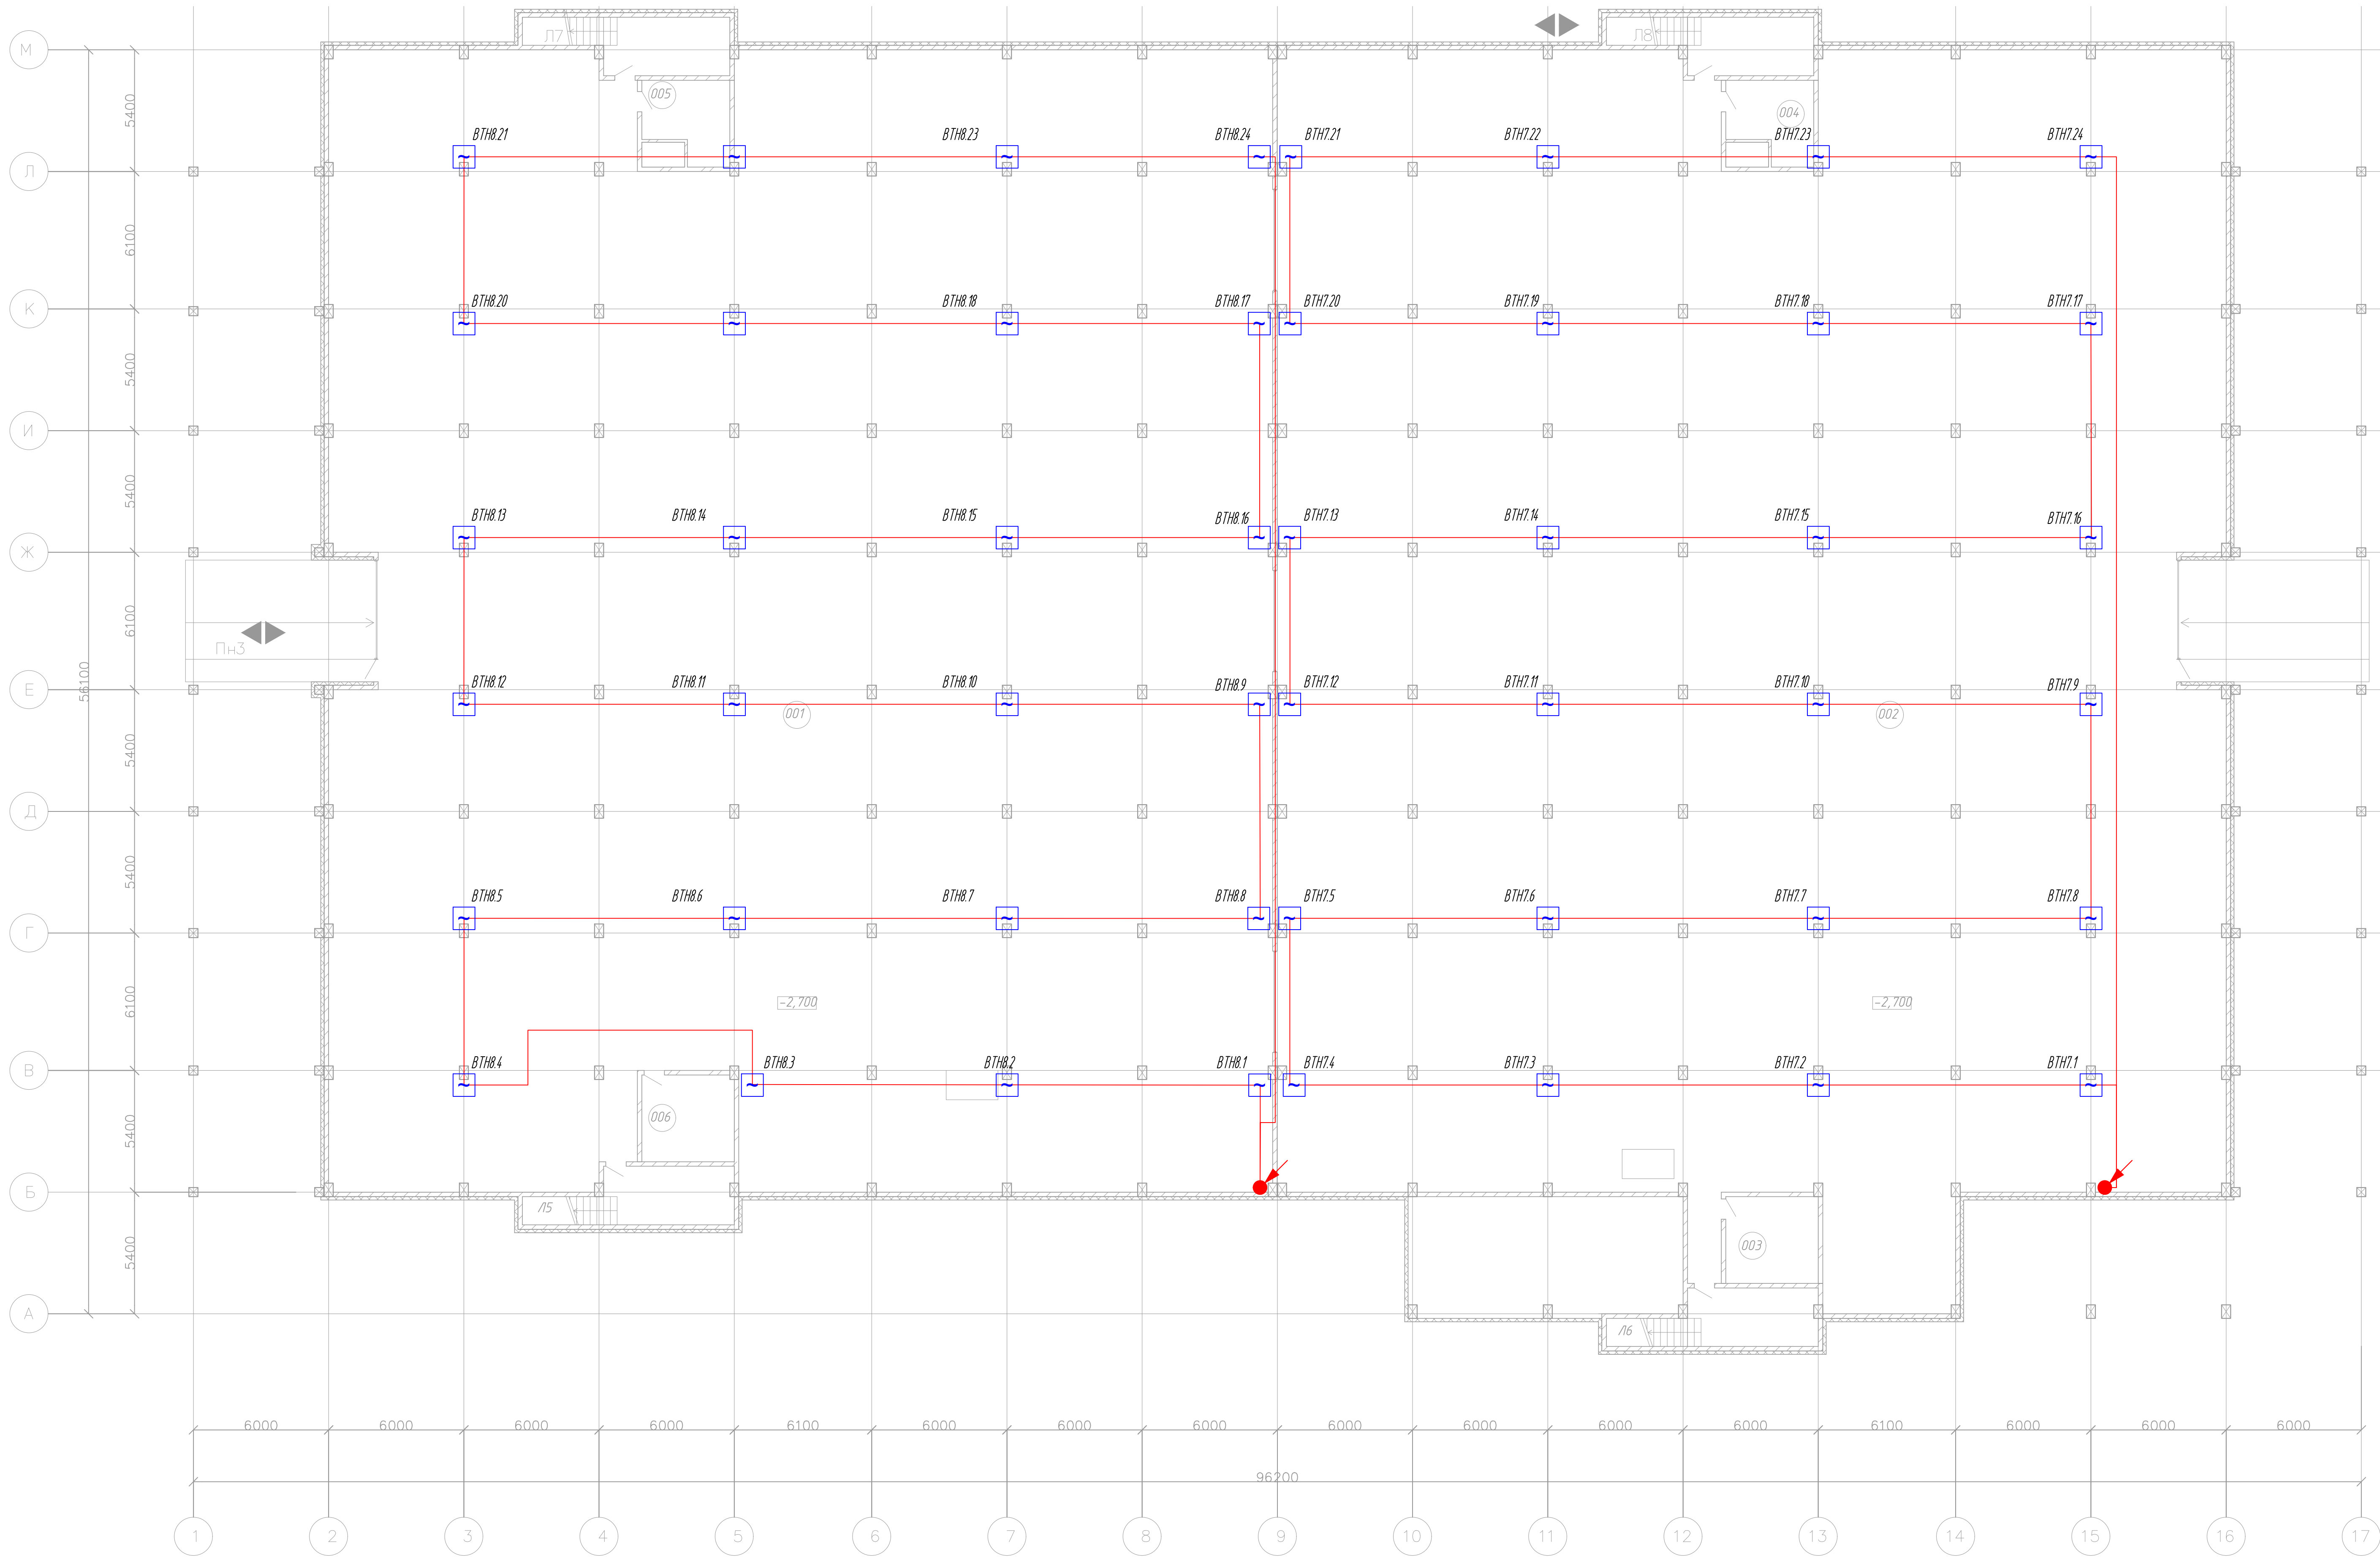


Общие данные см. 30.08.19-АПС.02
Условные обозначения см. 30.08.19-АПС.1

						Шифр: 30.08.19-АПС.3		
						Заказчик: ООО "Управляющая компания Прометей"		
						Новое строительство многоэтажного гаража-стоянки по адресу: г. Москва, Коробинское шоссе, вл.41 А, корп.1, корп.2		
Изм.	Кол. изм.	Лист	№ док.	Подп.	Дата	Автоматизация	Стадия	Лист
Разраб.	Нодиков	4.02.20					Р	1
Пров.	Ярмак И.Л.	17.02.20						6
						План расположения оборудования	ООО "Арт Нуво"	
Н. контр.	Румянцев	17.02.20						
ГИП	Ярмак И.Л.	17.02.20						

Экспликация помещений


№	Наименование помещений	Площадь м²	Категория взрывопожарной и пожарной опасности
101	Автостоянка №3	1982,2	В1
102	Автостоянка №4	2088,9	В1
103	Помещение охраны, диспетчерская	29,6	
104	Помещение слабых токов	10,9	В3
105	Электрощитовая	20,8	В3
106	Насосная	62,6	В4
107	Помещение хранения пож. инвентаря	12,7	В4
108	Пом. хранения уборочного инвентаря	12,7	В4
109	Помещение вент. установки	62,6	В1
110	Коридор	12,6	
111	С.у.	4,5	
112	С.у.	4,5	
113	Комната хранения багажа	25,9	В3
114	Помещение вент. установки	62,4	В1
115	Коридор	12,6	
116	С.у. для инвалидов	4,5	
117	С.у.	4,5	

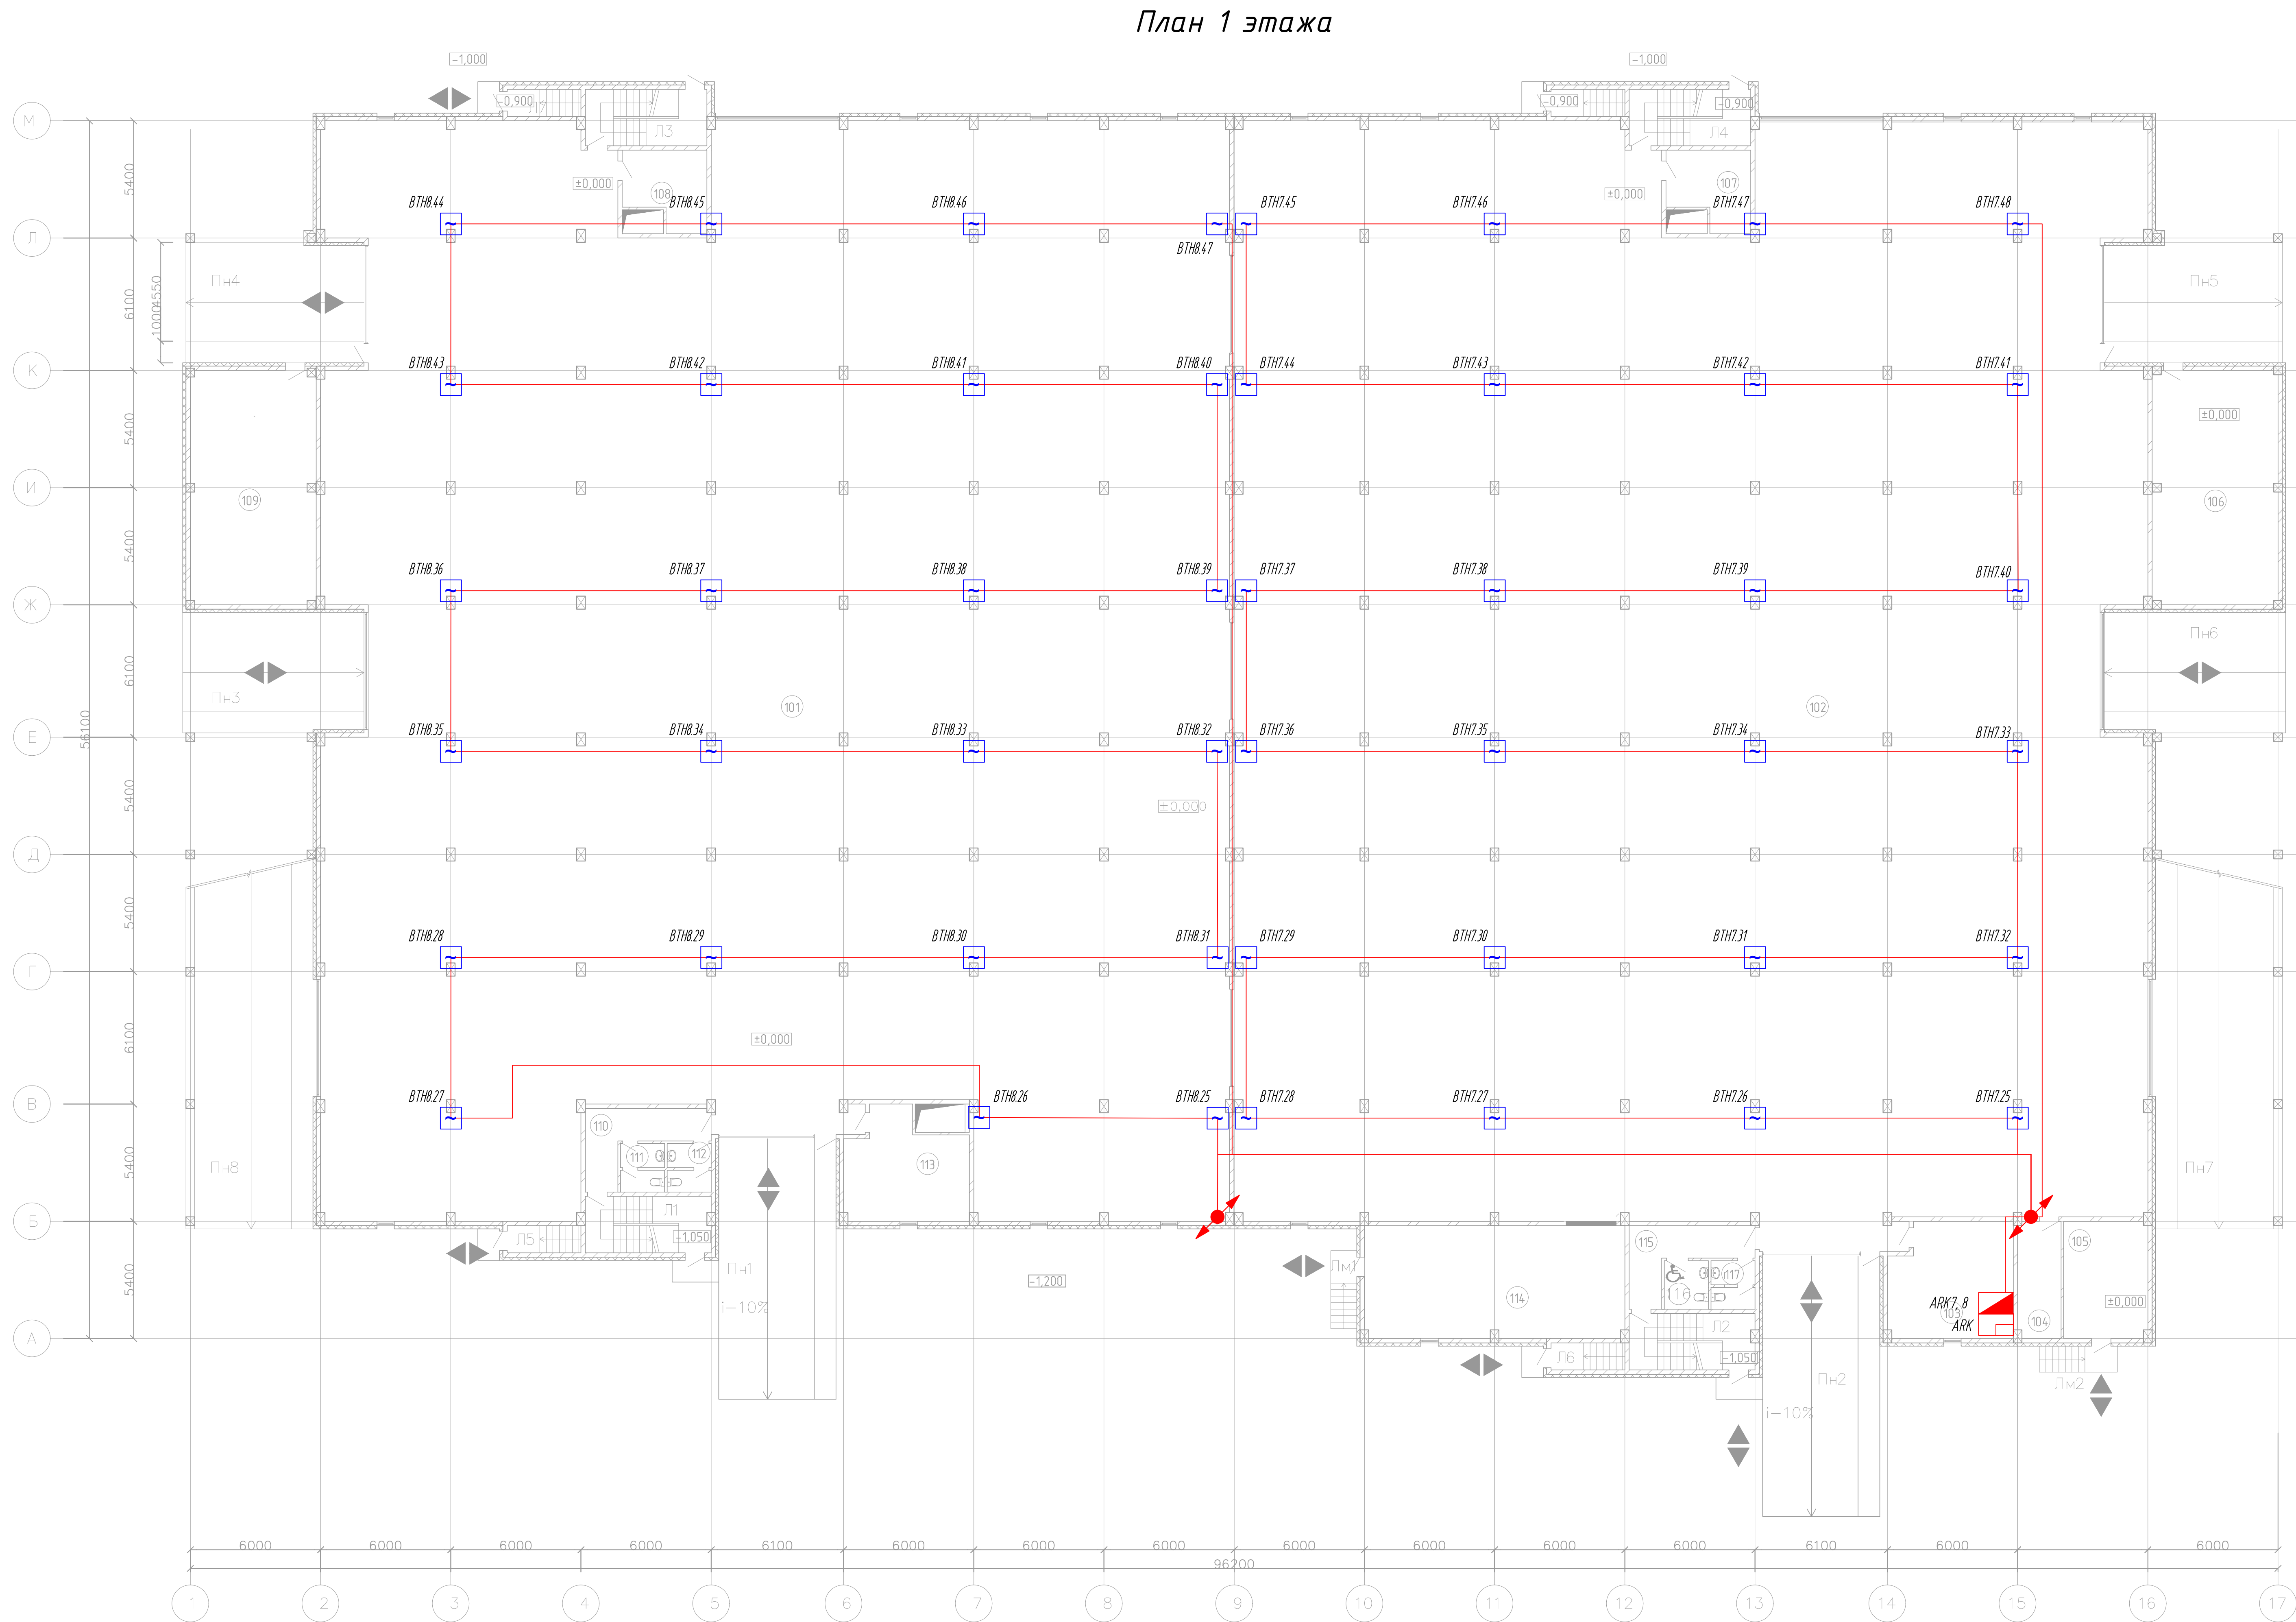

Согласовано					
Инв. № подл.	Взам. инв. №	Подпись и дата			

Шифр: 30.08.19-АПС.3					
Заказчик: ООО "Управляющая компания Прометей"					
Новое строительство многоэтажного гаража-стоянки по адресу: г. Москва, Коровинское шоссе, вл.41 А, корп.1, корп.2					
Изм.	Кол.уч.	Лист	№ док.	Подп.	Дата
Разраб.	Нодиков	4	12.20		
Проб.	Ярмак И.Л.	17	02.20		
Автоматизация				Стадия	Лист
				Р	2
План расположения оборудования				Листов 6	
Н.контр.	Румянцев	17	02.20	000 "Арт Нуво"	
ГИП	Ярмак И.Л.	17	02.20		


Экспликация помещений			
№	Наименование помещений	Площадь м²	Категория взрывопожарной и пожарной опасности
201	Автостоянка №5	2000,4	В1
202	Автостоянка №6	2120,3	В1
203	Пом. хранения уборочного инвентаря	31,2	В4
204	Вентиляционная камера	26,3	В1
205	Коридор	11,4	
206	С.у.	5,0	
207	С.у.	5,0	
208	Бухгалтерия	20,1	
209	Секретариат	28,5	
210	Дирекция	31,2	
211	Пом. хранения уборочного инвентаря	12,4	В4
212	Пом. хранения уборочного инвентаря	12,4	В4
213	Коридор	12,6	
214	С.у.	5,0	
215	С.у.	5,0	
216	Пом. хранения уборочного инвентаря	30,8	В4
217	Вентиляционная камера	27,5	В1

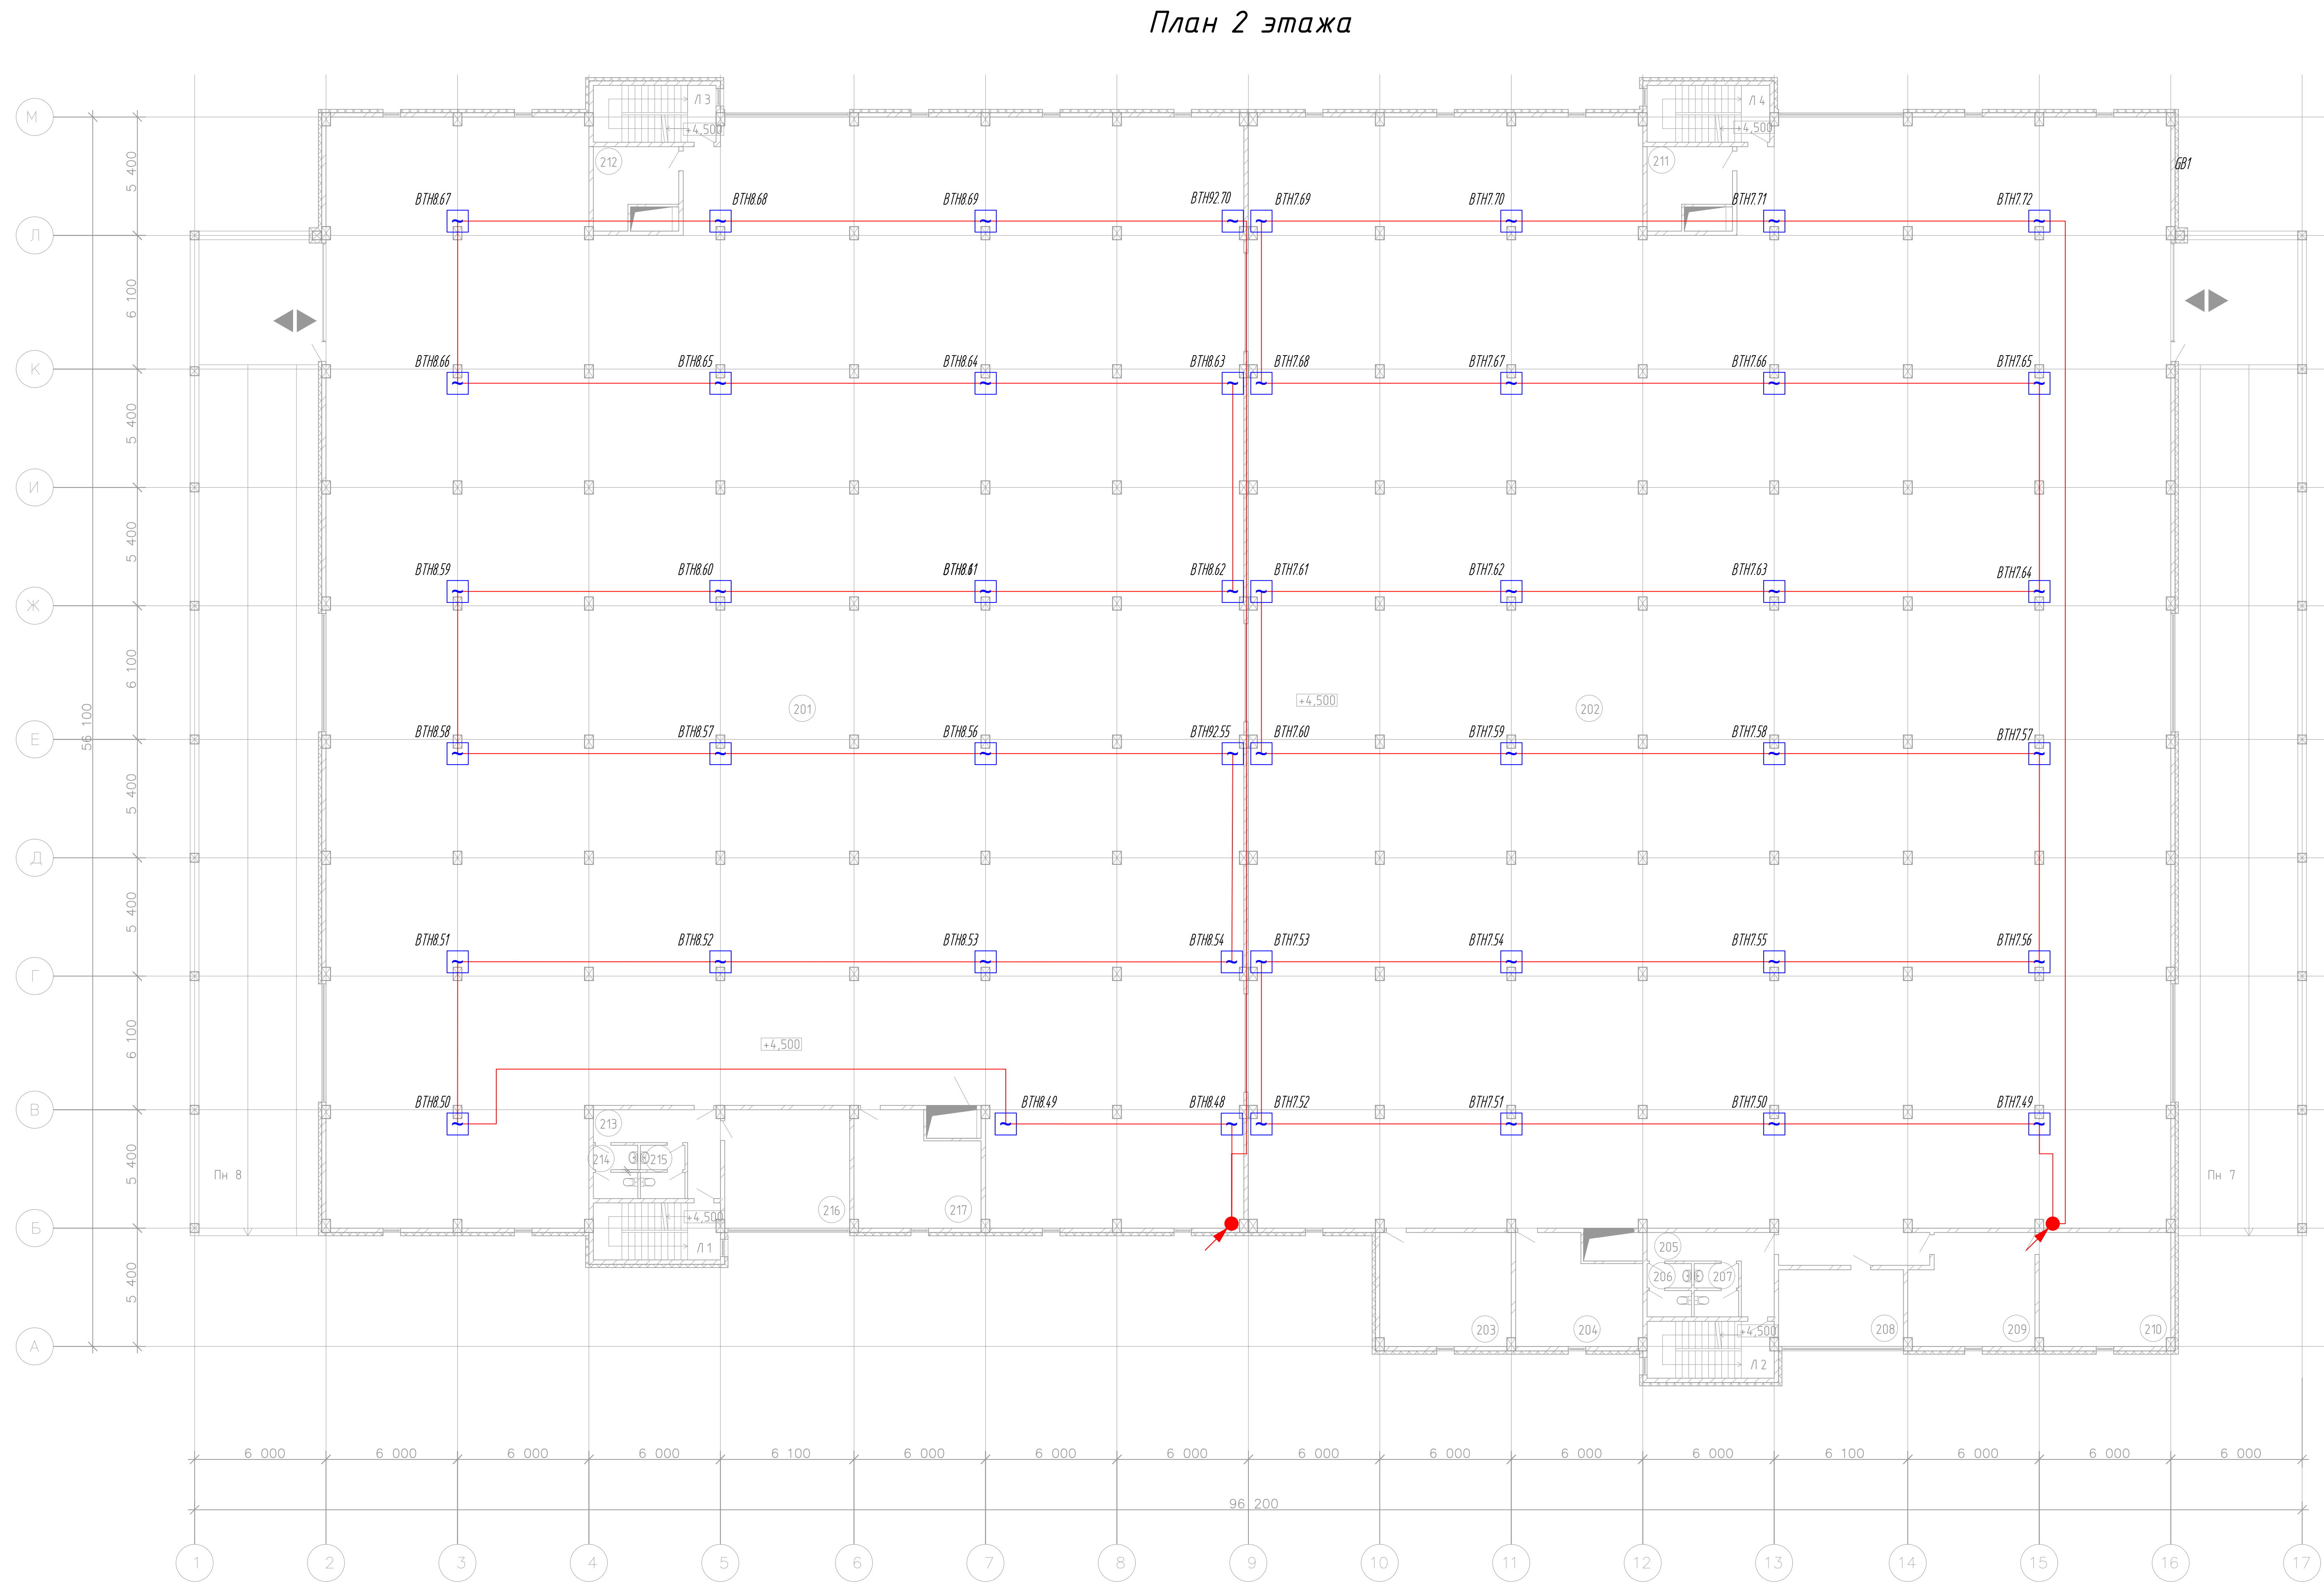

Согласовано					
Инв. № подл.	Подпись и дата	Взам. инв. №			


Изм.						Шифр:			30.08.19-АПС.3		
Разраб.						Заказчик:			ООО "Управляющая компания Прометей"		
Пров.						Новое строительство многоэтажного гаража-стоянки по адресу: г. Москва, Коробинское шоссе, вл.41 А, корп.1, корп.2					
						Автоматизация			Стадия	Лист	Листов
									Р	3	6
Н.контр.						План расположения оборудования			ООО "Арт Нуво"		
ГИП											

№	Наименование помещений	Площадь м ²	Категория взрывопожарной и пожарной опасности
001	Автостоянка №1	2057,6	В1
002	Автостоянка №2	2133,3	В1
003	Помещение хранения пож. инвентаря	16,0	В4
004	Пом. хранения уборочного инвентаря	12,7	В4
005	Пом. хранения уборочного инвентаря	12,7	В4
006	Помещение хранения пож. инвентаря	15,9	В4

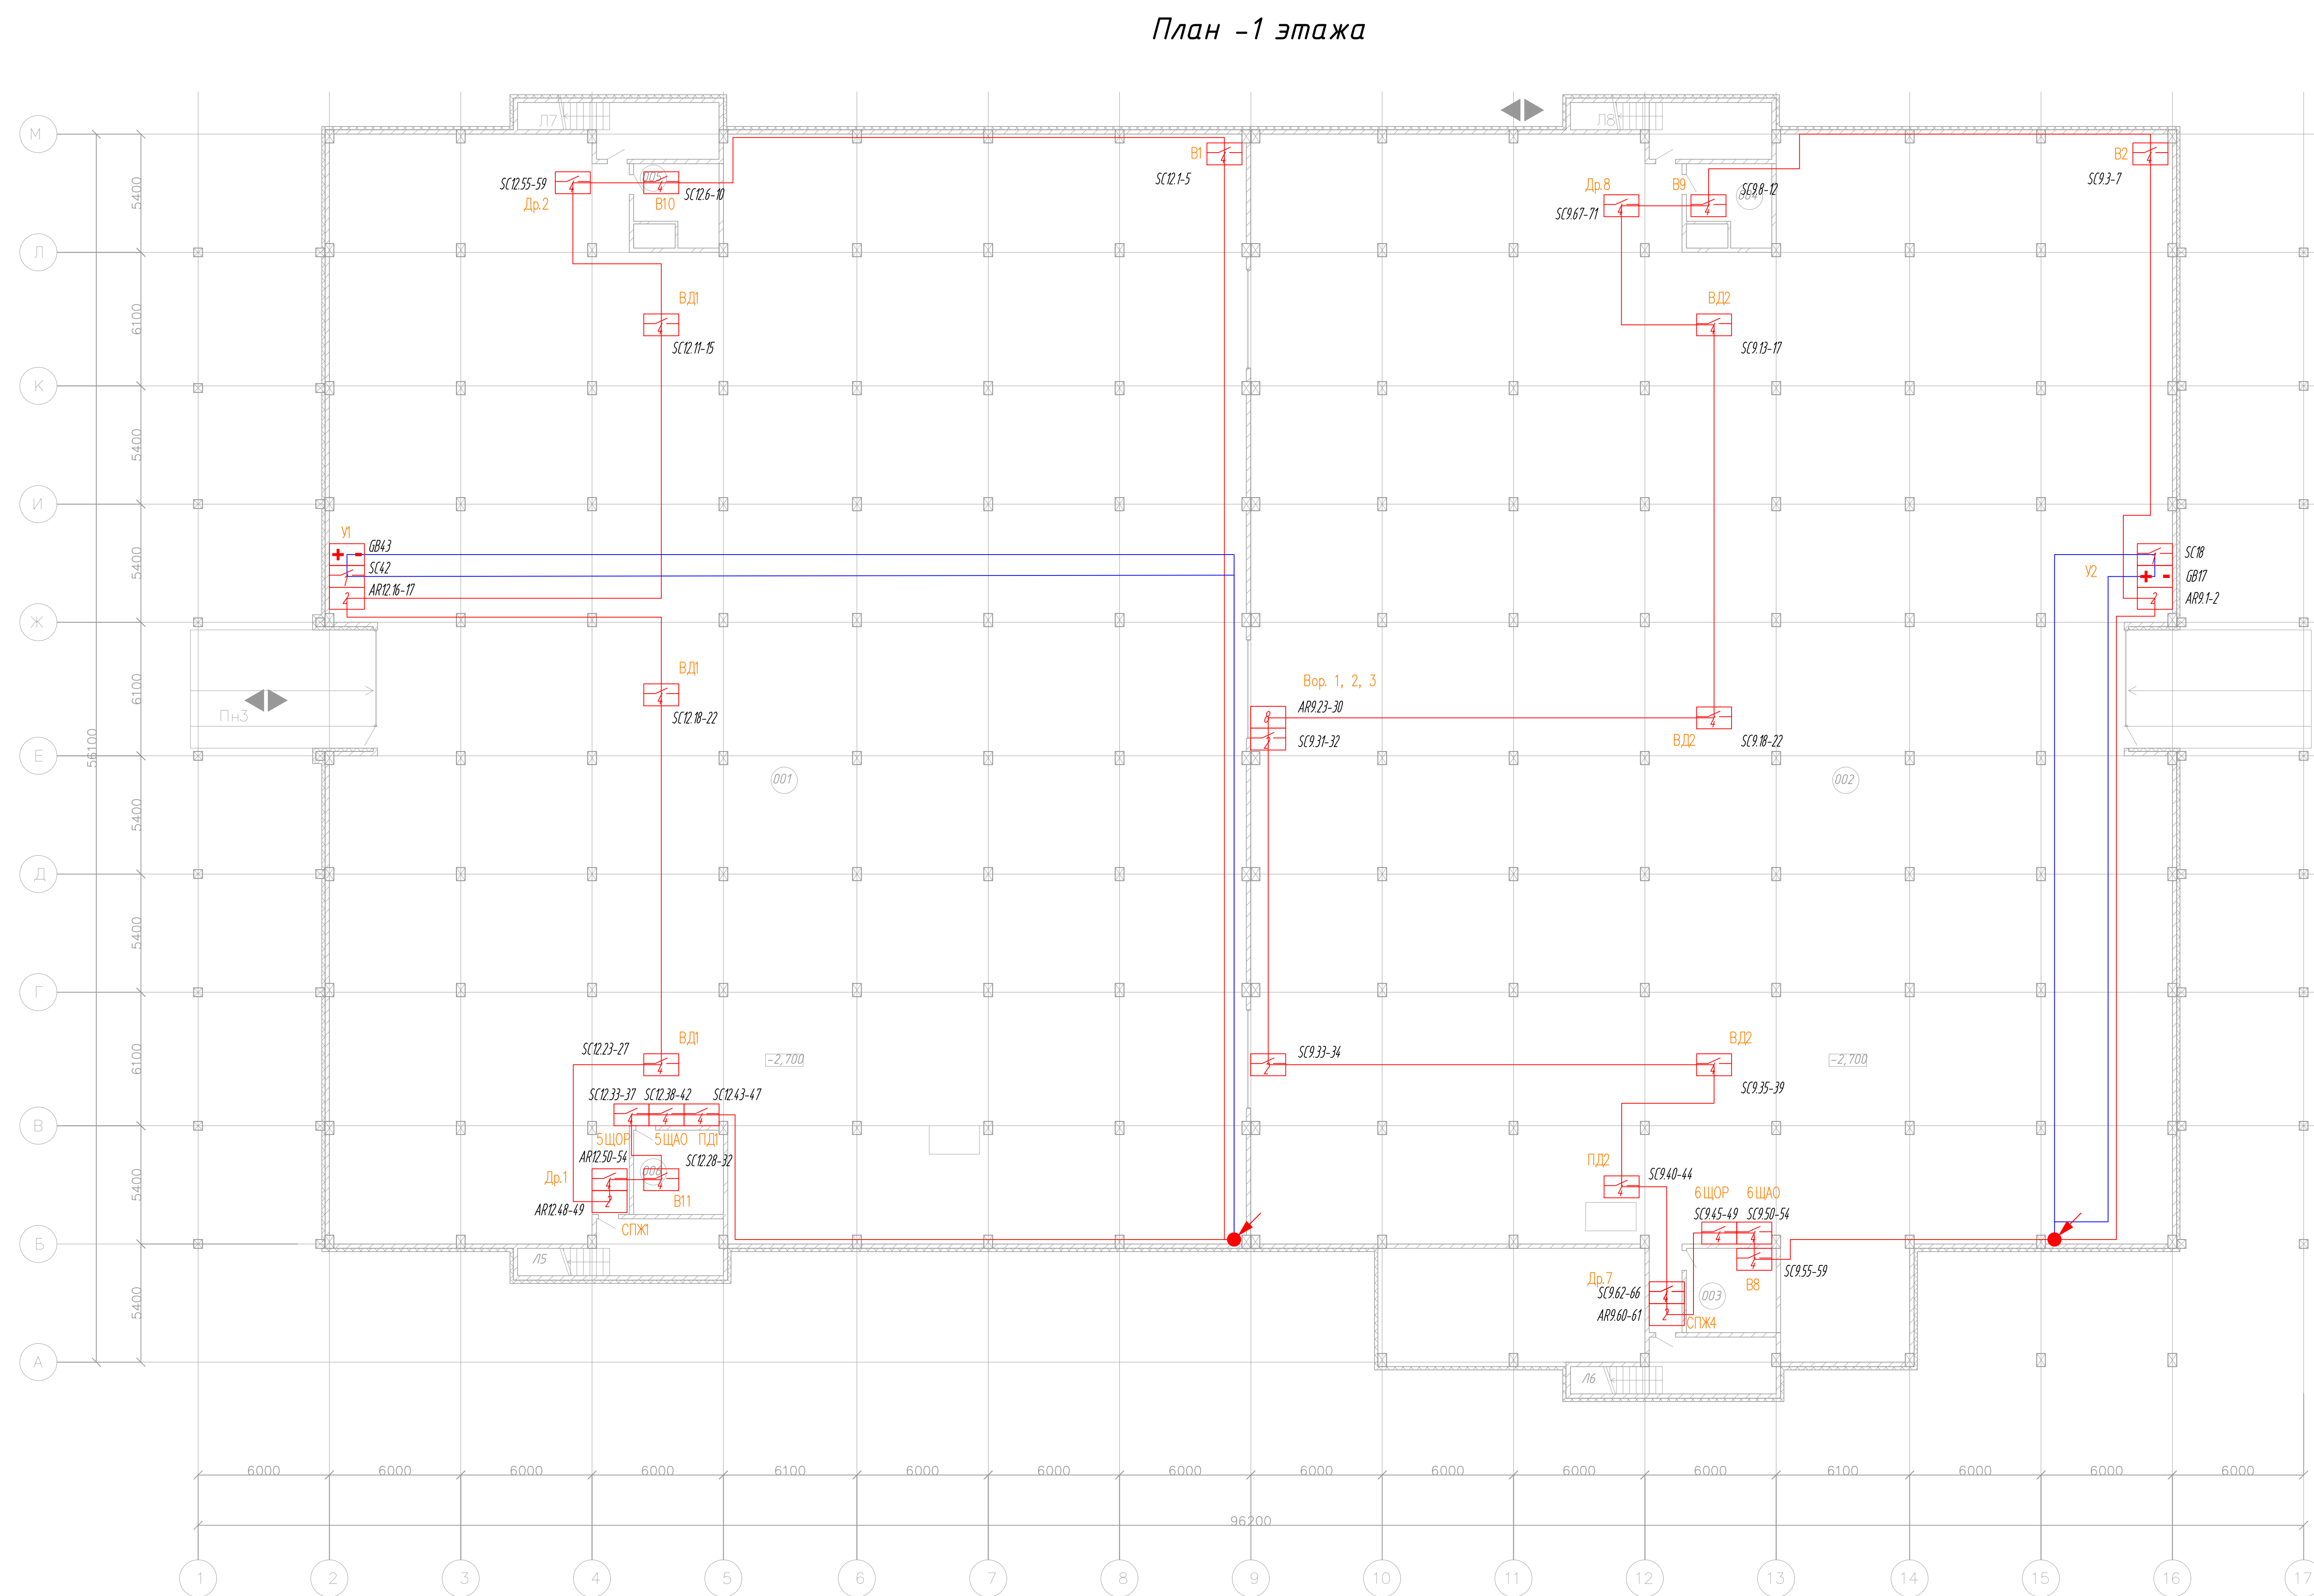

						Шифр: 30.08.19-АП.3 Заказчик: ООО "Управляющая компания Прометей"			
						Новое строительство многоэтажного здания-стоянки по адресу: г. Москва, Коровинское шоссе, вл.41 А, корп.1, корп.2			
Изм.	Кол.уч.	Лист	№ док.	Подп.	Дата	Автоматизация	Стадия	Лист	Листов
Разраб.		Новиков			07.02.20				
Пров.		Ярмак И.И.			07.02.20		Р	4	6
						План расположения оборудования	ООО "Арт Нуво"		
Н.контр.		Румянцев			07.02.20				
Гипр.		Ярмак И.И.			07.02.20				

Экспликация помещений			
№	Наименование помещений	Площадь м²	Категория взрывопожарной и пожарной опасности
101	Автостоянка №3	1982,2	В1
102	Автостоянка №4	2088,9	В1
103	Помещение охраны, диспетчерская	29,6	
104	Помещение слабых токов	10,9	В3
105	Электрощитовая	20,8	В3
106	Насосная	62,6	В4
107	Помещение хранения пож. инвентаря	12,7	В4
108	Пом. хранения уборочного инвентаря	12,7	В4
109	Помещение вент. установки	62,6	В1
110	Коридор	12,6	
111	С.у.	4,5	
112	С.у.	4,5	
113	Комната хранения багажа	25,9	В3
114	Помещение вент. установки	62,4	В1
115	Коридор	12,6	
116	С.у. для инвалидов	4,5	
117	С.у.	4,5	

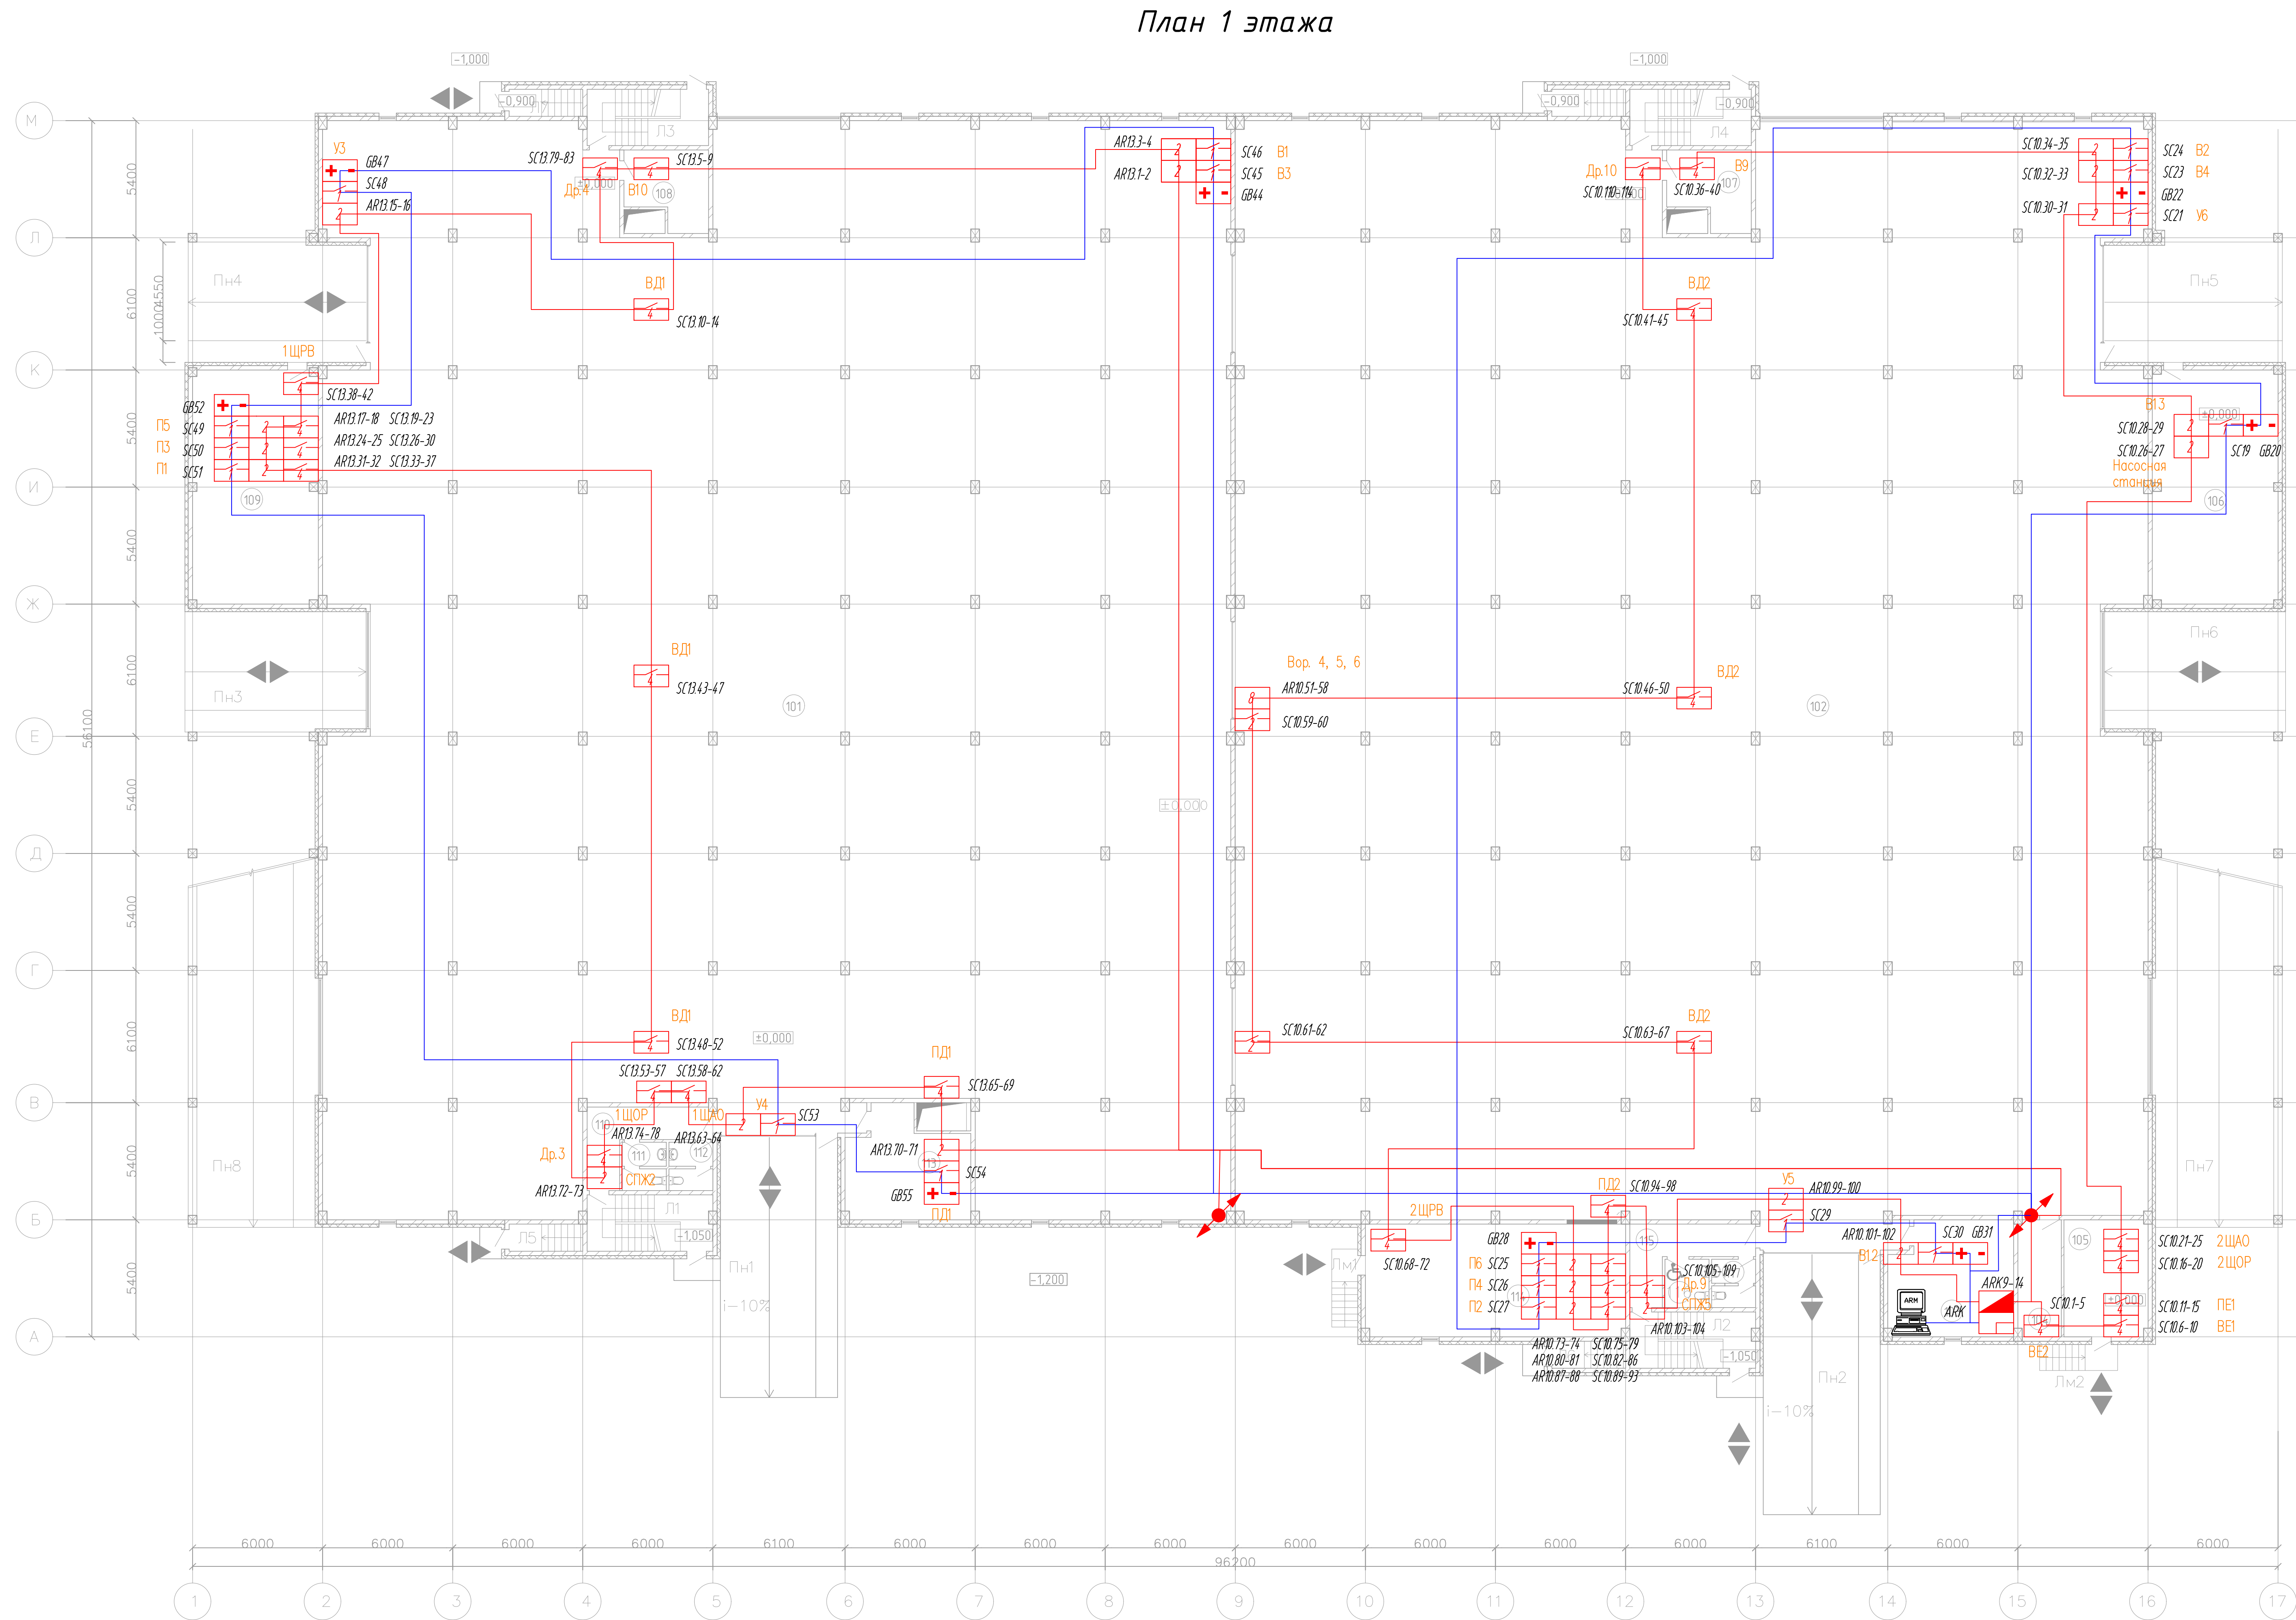


						Шифр: 30.08.19-АПС.3			
						Заказчик: ООО "Управляющая компания Прометей"			
Новое строительство многоэтажного гаража –стоянки по адресу: г. Москва, Коровинское шоссе, вл.41 А, корп.1, корп.2									
Изм.	Кол. изм.	Лист	№ док.	Подп.	Дата	Автоматизация	Стадия	Лист	Листов
Разраб.		Новиков			17.02.20		Р	5	6
Проб.		Ярмак И. П.			17.02.20				
Н контр.		Румянцев			17.02.20	План расположения оборудования	ООО "Арт Нуво"		
ГИП		Ярмак И. П.			17.02.20				

План 2 этажа

Экспликация помещения

№	Наименование помещений	Площадь м²	Категория взрывопожарной и пожарной опасности
201	Адвостоянка №5	2000,4	В1
202	Адвостоянка №6	2120,3	В1
203	Пом. хранения уборочного инвентаря	31,2	В4
204	Вентиляционная камера	26,3	В1
205	Коридор	11,4	
206	С.у.	5,0	
207	С.у.	5,0	
208	Бухгалтерия	20,1	
209	Секретариат	28,5	
210	Дирекция	31,2	
211	Пом. хранения уборочного инвентаря	12,4	В4
212	Пом. хранения уборочного инвентаря	12,4	В4
213	Коридор	12,6	
214	С.у.	5,0	
215	С.у.	5,0	
216	Пом. хранения уборочного инвентаря	30,8	В4
217	Вентиляционная камера	27,5	В1

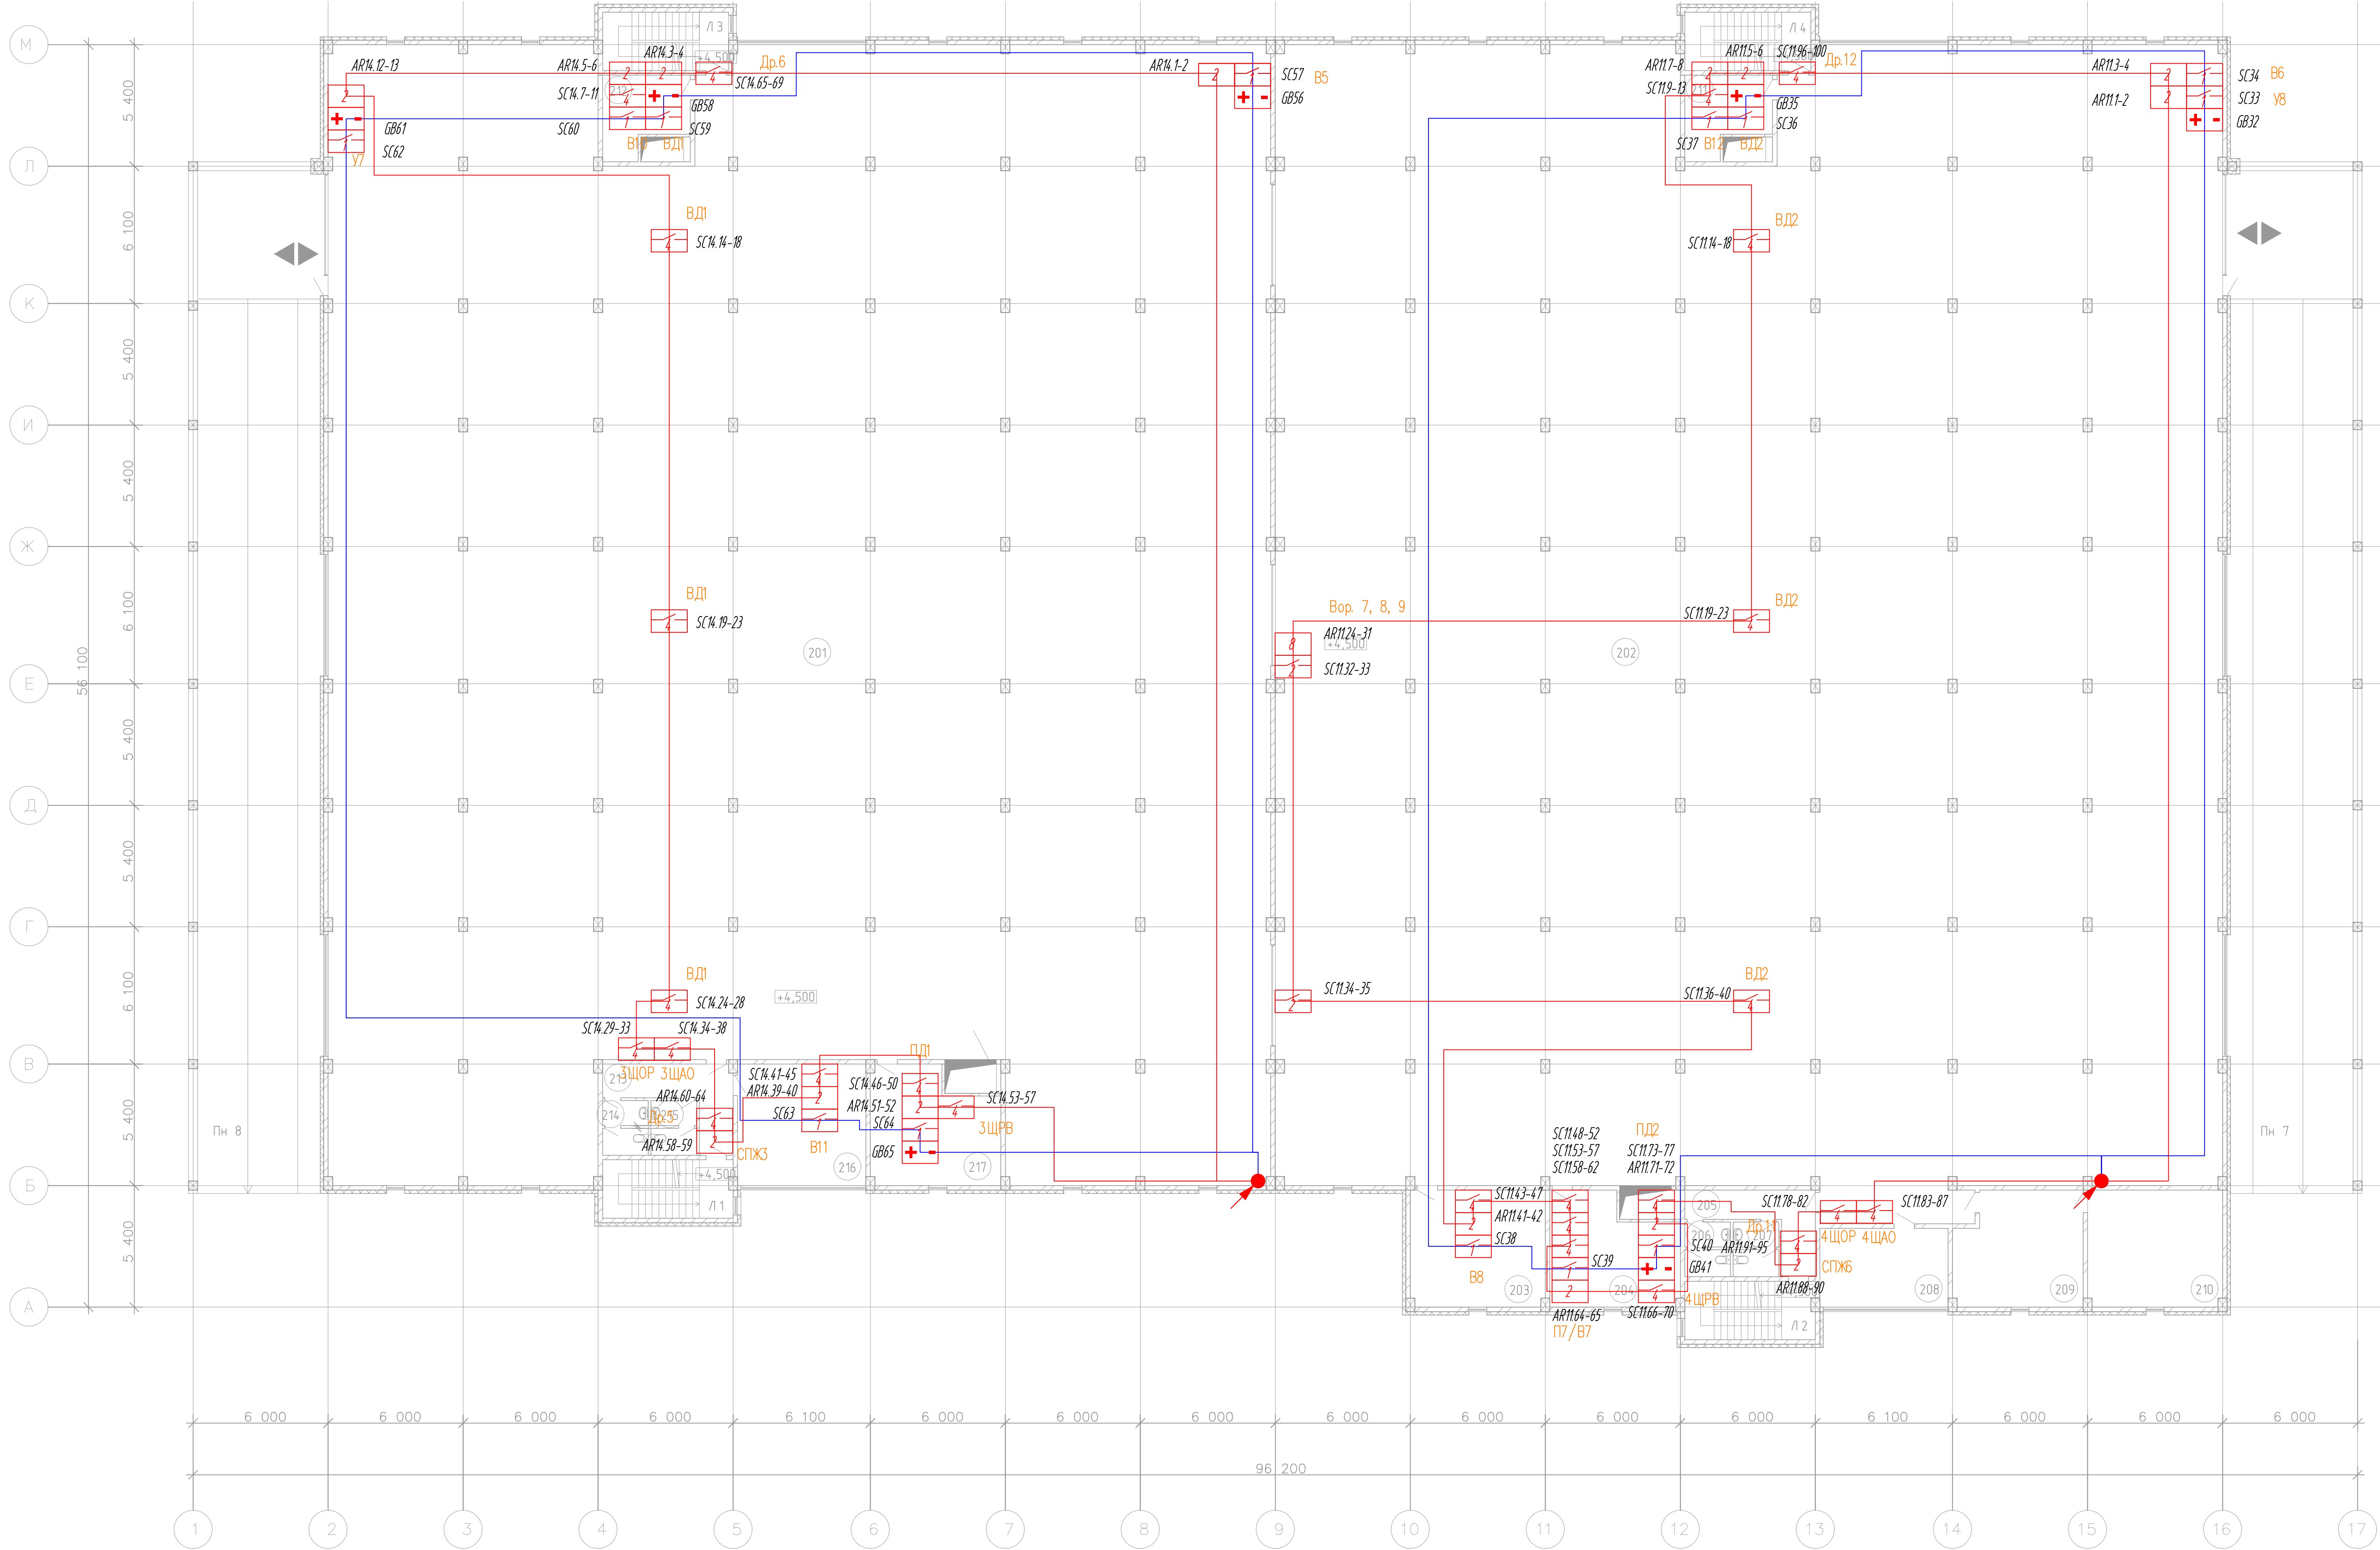

						Шифр: 30.08.19-АП.3			
						Заказчик: ООО "Управляющая компания Прометей"			
Новое строительство многоэтажного здания-стоянки по адресу: г. Москва, Кордовинское шоссе, вл.4/1 А, корп.1, корп.2									
Изм.	Кол. изм.	Лист	№ док.	Подп.	Дата	Автоматизация			
Разраб.		Новиков			17.02.20	Стадия	Лист	Листов	
Пров.		Ярмак И. П.			17.02.20	Р	6	6	
Н. контр.		Румянцев			17.02.20	План расположения оборудования			
ГИП		Ярмак И. П.			17.02.20	ООО "Арт Нубо"			

				№ п.п.	Наименование и техническая характеристика			Тип, марка, обозначение документа, опросного листа			Код продукции		Поставщик		Ед. измерения	Кол.	Масса 1 ед., кг	Примечание	
				1	2			3			4		5		6	7	8	9	
					Оборудование	
				1	Пульт контроля и управления			С2000М					НВП «Болид»		шт.	1	0,3	
				2	Контроллер двухпроводной линии			С2000-КДЛ-2И					НВП «Болид»		шт.	14	0,3	
				3	Устройство оконечное объектовое системы передачи извещений			С2000-PGE					НВП «Болид»		шт.	1	0,2	
				4	Преобразователь интерфейса			С2000-ПИ					НВП «Болид»		шт.	2	0,2	
				5	Блок сигнально-пусковой адресный			С2000-СП4/220					НВП «Болид»		шт.	75	0,3	
				6	Блок сигнально-пусковой адресный			С2000-СП2					НВП «Болид»		шт.	6	0,3	
				7	Блок сигнально-пусковой адресный			С2000-СП1 исп. 01					НВП «Болид»		шт.	32	0,3	
				8	Адресный расширитель			С2000-АР8					НВП «Болид»		шт.	3	0,2	
				9	Адресный расширитель			С2000-АР2					НВП «Болид»		шт.	39	0,2	
				10	Извещатель пожарный дымовой оптико-электронный адресно-аналоговый			ДИП-34А-03					НВП «Болид»		шт.	573	0,1	
				11	Извещатель пожарный дымовой оптико-электронный адресно-аналоговый с изолятором короткого замыкания			ДИП-34А-04					НВП «Болид»		шт.	24	0,1	
				12	Извещатель пожарный ручной адресный			ИПР 513-ЗАМ					НВП «Болид»		шт.	44	0,1	
				13	Извещатель пожарный комбинированный адресно-аналоговый газовый			С2000-ИПГ					НВП «Болид»		шт.	142	0,1	
				14	Извещатель магнито-контактный для металлических поверхностей			ИО 102-26 исп.06 "Змея"					Россия		шт.	18	0,1	
				15	Резервированный источник питания РИП-24 исп.50			РИП-24 исп.50					НВП «Болид»		шт.	19	2,5	
				16	Аккумулятор			12 В 7 А/ч					Россия		шт.	38	2,5	
				17	Сервер для охранно-пожарной сигнализации и системы контроля доступа			ОПС-СКД127 исп.02					НВП «Болид»		шт.	1	27	
Согласовано	

№ п.п.	Наименование и техническая характеристика	Тип, марка, обозначение документа, опросного листа	Код продукции	Поставщик	Ед. измерения	Кол.	Масса 1 ед., кг	Примечание		
1	2	3	4	5	6	7	8	9		
18	Монитор	Acer ET241Ybd 24"		Россия	шт.	2	3,9			
	Кабели и провода									
19	Кабель	КПСВэВнг-FRHF 1x2x1,5		Россия	м	8115	0,072			
20	Кабель	КПСВэВнг-FRHF 2x2x1,0		Россия	м	1170	0,068			
	Материалы									
21	Труба водо-газопроводная	37x2,5		Россия	м	40	2,13			
22	Труба жесткая гладкая ПВХ, DN=25 мм			Россия	м	6560	0,135			
23	Муфта соединительная D=25 мм, труба-труба			Россия	шт.	3250	0,029			
24	Угол 90° открывающийся D=25 мм, труба-труба			Россия	шт.	524	0,004			
25	Тройник открывающийся D=25 мм, труба-труба			Россия	шт.	641	0,008			
26	Кабель-канал электротехнический 100x50			Россия	м	10	0,35			
27	Угол плоский 100x50			Россия	шт.	4	0,1			
28	Кабель-канал электротехнический 20x10			Россия	м	15	0,1			
29	Угол 20x10			Россия	шт.	4	0,005			
30	Скоба оцинкованная двухлапковая D25			Россия	шт.	21600	0,005			
31	Скоба оцинкованная двухлапковая D32			Россия	шт.	120	0,006			
32	Коробка протяжная	У-994		Россия	шт.	8	0,35			
33	Распаеячная коробка ОП	ОП 80x80x50		Россия	шт.	18	0,2			
Взам. инв. №								Шифр: 30.08.19-АПС.СО		Лист
										2
Подп. и дата										
Инв. № подл.										
		Изм.	Кол.уч	Лист	№ док.	Подпись	Дата			

Инв. № подл.	Подп. и дата	Взам. инв. №

№ п.п.	Наименование и техническая характеристика	Тип, марка, обозначение документа, опросного листа	Код продукции	Поставщик	Ед. измерения	Кол.	Масса 1 ед., кг	Примечание
1	2	3	4	5	6	7	8	9
34	Коробка монтажная огнестойкая	КМ-О (4к)-IP41		Россия	шт.	18	0,1	
35	Крепеж			Россия	кг	10		

						Шифр: 30.08.19-АПС.СО	Лист
							3
Изм.	Кол.уч	Лист	№ док.	Подпись	Дата		